苗栗縣立永貞國民小學

115年度圖書館空間改善工程

細部設計圖

張薰和建築師事務所

中華民國115年08月

115年度圖書館空間改善工程

圖　　目　　錄

圖　號	圖　　名
01 － 32	圖目錄、工程告示牌
02 － 32	工程位置圖、施工注意事項要點
03 － 32	現況及結構物拆除示意圖
04 － 32	既有燈具及電扇拆除示意圖
05 － 32	平面配置圖
06 － 32	新設燈具配置圖(一)
07 － 32	新設燈具迴路圖
08 － 32	新設燈具配置圖(照度分析)
09 － 32	平面配置圖(二)
10 － 32	新設電源網路配置圖
11 － 32	監視器平面圖
12 － 32	立面索引圖
13 － 32	A向立面圖
14 － 32	B向立面圖
15 － 32	C向立面圖
16 － 32	D向立面圖
17 － 32	入口意象設計圖
18 － 32	入口意象設計圖(二)
19 － 32	服務櫃台設計圖
20 － 32	木作造型推拉門設計圖
21 － 32	大窩居/小窩居設計圖
22 － 32	造型主題/雜誌書櫃、造型矮凳設計圖
23 － 32	舞台、理書區高櫃設計圖
24 － 32	電信設備櫃設計圖
25 － 32	廣播、監視系統設計圖
26 － 32	保全及電箱設備櫃、圖書區高書櫃設計圖
27 － 32	理書區、舞台區、靠窗邊、圖書區-系統開放矮櫃詳圖
28 － 32	燈具及電扇設計圖
29 － 32	油漆、防焰捲簾、PVC地磚、窗邊討論桌、檢索桌設計圖
30 － 32	討論桌、辦公椅、討論椅、書報架設計圖
31 － 32	入口意象、造型窩居示意圖
32 － 32	3D示意圖

120

苗栗縣立永貞國民小學　(Sanwan Junior High School,Miaoli County)

工程名稱 (Project Name)	115年度圖書館空間改善工程		
監造單位 (Construction Supervisor)	世京工程顧問有限公司	設計單位 (Designer)	世京工程顧問有限公司
施工廠商 (Contractor)		工程概要 (Project Descriptions)	
施工期間 (Duration)	民國115年00月00日至115年00月00日 (DD/MM/YYYY~ DD/MM/YYYY)		
工地負責人 (Site Manager)		電話 (TEL)	
專任工程人員 (Contractor's Professional Engineer)		電話 (TEL)	
通報專線 (Complaints & Suggestions)	全民督工專線及網址 (Hot Line and Web Site)	0800-009-609 http://www.pcc.gov.tw 督工通報行動版	
	政風單位(Government Ethics Department)	037-831002	
契約經費及來源 (Contract Price and Sources)	1.中央(The Central)：「○○○計畫」（千元）(Unit:NT$1,000) 2.地方(The Local)：（千元）(Unit:NT$1,000)		
重要公告事項 (Notice)	1.空氣污染防制費徵收管制編號(The Construction Project Air Pollution Control Fee Collection Control Serial Number)： 2.公害檢舉電話號碼(The Telephone Number for Notifying Public Nuisances)： 3.__年(Yr)__月(M)__日(D)：		

工程告示牌正視圖　單位：CM　S=N

1. 漆綠色底，白色圖目錄正楷字體白色線條及框。
2. 各框格之大小參照圖示尺寸。
3. 工程竣工驗收後,告示牌由承包商負責予以移除。

工程名稱 PROJECT

永貞國小圖書館整修工程

圖號 DRAWNG NO.	張號 SHEET NO.
	1/32

圖面修正 REVISISONS

NO.	日期 DATE	內容 REMARKS

圖面名稱 DRAWNGTITLE

圖目錄、工程告示牌

張薰和建築師事務所

苗栗市國華路158號2樓

電話:037-263019

傳真:037-263851

圖說 NOTE

起造人及承造人應守事項

1.起造人於施工前,應請地政機關鑑定界址,所有尺寸以地政機關鑑界為準,依照實際基地範圍內配合政府所指定建築線施工,不得越界侵佔鄰地,更勿擅自先行動工,否則如有糾紛或受罰,由起造人自行負法律責任.

2.本設計圖經核准後,起造人及承造人必須申報開工,按圖施工,並按進度邀請審驗報告,以備完工時申領使用執照.

3.請切實按核准圖樣施工,如原計劃有未盡理想之處,欲予變更時,務須事先辦理變更設計手續,經核准後再行施工,以符法令,切勿擅自變更,否則其後果由起造人承造人負全責.

4.建造房屋必須請合法且無欠稅之營造廠承造.

5.所有基礎,樑柱,樓地板,鋼筋,裝妥後,請起造人知會建築師查驗合格後,才准灌注混凝土.

6.必須注意鄰居房屋之安全,及行人之安全,並不可將建築物材料堆置於道路上妨礙交通.

7.房屋完工後,立即拆除工寮,並將房屋周圍道路水溝清理修復,然後由承造廠商申請核發使用執照,再憑使用執照申請接通水電設備.

8.如有其他臨時發生之疑問,請即提出研討或向縣市政府建管單位書面查詢,切勿擅自解釋主令或施做.

9.承造人不得使用下列材料:　(1) 海砂　(2) 輻射鋼筋

比例 SCALE	
設計 DESIGN BY	
繪圖 DRAWN BY	
校對 CHECK BY	
核准 APPROVED BY	
日期 DATE	



工程施工注意事項要點:

一	得標廠商應依契約及監造計畫每周提送施工日誌及相關自主檢查表單。
二	各施工項目，如:基礎整理、土方開挖、土方回填、混凝土澆置、模板組立、鋼筋組立、基礎螺栓埋設等各隱蔽部份，均須於該項工程施工之前一工作天，通知監造單位到場查驗無誤後，方可繼續施工。並於每周一提送上周日誌及相關檢查表。
三	如施工時發生用地問題，請連絡甲方(苗栗縣立永貞國民小學　　)及設計監造單位擇期會勘，待解決方案確定後再行施工。
四	承包廠商於施工呈報竣工前，應通知監造單位確認核章後方可申報竣工。
五	如有未盡事宜，依工程合約及施工規範辦理之。
六	以上各點請承包廠商確實執行，如未確實執行因而衍生相關施工問題及法律責任等，概由承包廠商自行負責。
七	承商申報竣工前，應標示里程樁號以利辦理初驗及備妥下列四項。 (1)完工報告書。 (2)施工前、中、後(各個結構物)相片。(3)各項材料試驗報告及出廠證明(合約無者免附)。 (4)自主檢查表。
八	相關結算資料提送份數依工程契約規定惟需包含乙份正本為原則。
九	本工程所採用材料，得以使用同等品，使用同等品須提送對照資料以供監造及主辦單位審核，審核通過即可使用同等品。
十	本工程各主要工項使用材料及相關證明，應依圖說內容送審，經監造單位及主辦機關審核後，方可進場施工，如材料品質及質感與送審資料不符，需退貨並重新進料。
十一	本工程除設計圖上另有註明者外，均依施工說明書辦理，如有未盡事宜依監造人員指示辦理。
十二	本工程如有廢方應處理者，請「勿隨意回填而影響當地環境，且應循合法途徑辦理」。
十三	施工便道及復舊部分應於完成裸露坡面敷、覆蓋作業，藉以保護坡面。
十四	本案施工時，應以『順應原地形開挖並減少裸露面為原則』。
十五	本圖說如相關尺寸標示不清，則依設計單位解釋為主，現場高程或相關現地變化與設計圖有差異時，請通知設計或監造單位到場勘查，待相關人員現場確認後再行施工。

工程名稱 PROJECT

永貞國小圖書館整修工程

圖號 DRAWNG NO.	張號 SHEET NO.
	2/32

圖面修正 REVISISONS

NO.	日期 DATE	內容 REMARKS

圖面名稱 DRAWNGTITLE


工程位置圖、施工注意事項要點

張薰和建築師事務所
苗栗市國華路158號2樓
電話:037-263019
傳真:037-263851

圖 說 NOTE

起造人及承造人應守事項
1.起造人於施工前,應請地政機關鑑定界址,所有尺寸以地政機關鑑界為準,依照實際基地範圍內配合政府所指定建築線施工,不得越界侵佔鄰地,更勿擅自先行動工,否則如有糾紛或受罰,由起造人自行負法律責任.
2.本設計圖經核准後,起造人及承造人必須申報開工,按圖施工,並按進度提請查驗報告,以備完工時申領使用執照.
3.請切實按核准圖樣施工,如原計劃有未盡理想之處,欲予變更時,務須事先辦理變更設計手續,經核准後再行施工,以符法令,切勿擅自變更,否則其後果由起造人承造人負全責.
4.建造房屋必須請合法且無欠稅之營造廠承造.
5.所有基礎,樑柱,樓地板,鋼筋,裝妥後,請起造人知會建築師簽證合格後,才准灌注混凝土.
6.必須注意鄰居房屋之安全,及行人之安全,並不可將建築物材料堆置於道路上妨礙交通.
7.房屋完工後,立即拆除工寮,並將房屋周圍道路水溝清理修復,然後由承造廠商申請核發使用執照,再憑使用執照申請接通水電設備.
8.如有其他臨時發生之疑問,請即提出研討或向縣市政府建築單位書面查詢,切勿擅自解釋主令或施做.
9.承造人不得使用下列材料: (1) 海砂 (2) 輻射鋼筋

比例 SCALE	
設計 DESIGN BY	
繪圖 DRAWN BY	
校對 CHECK BY	
核准 APPROVED BY	
日期 DATE	

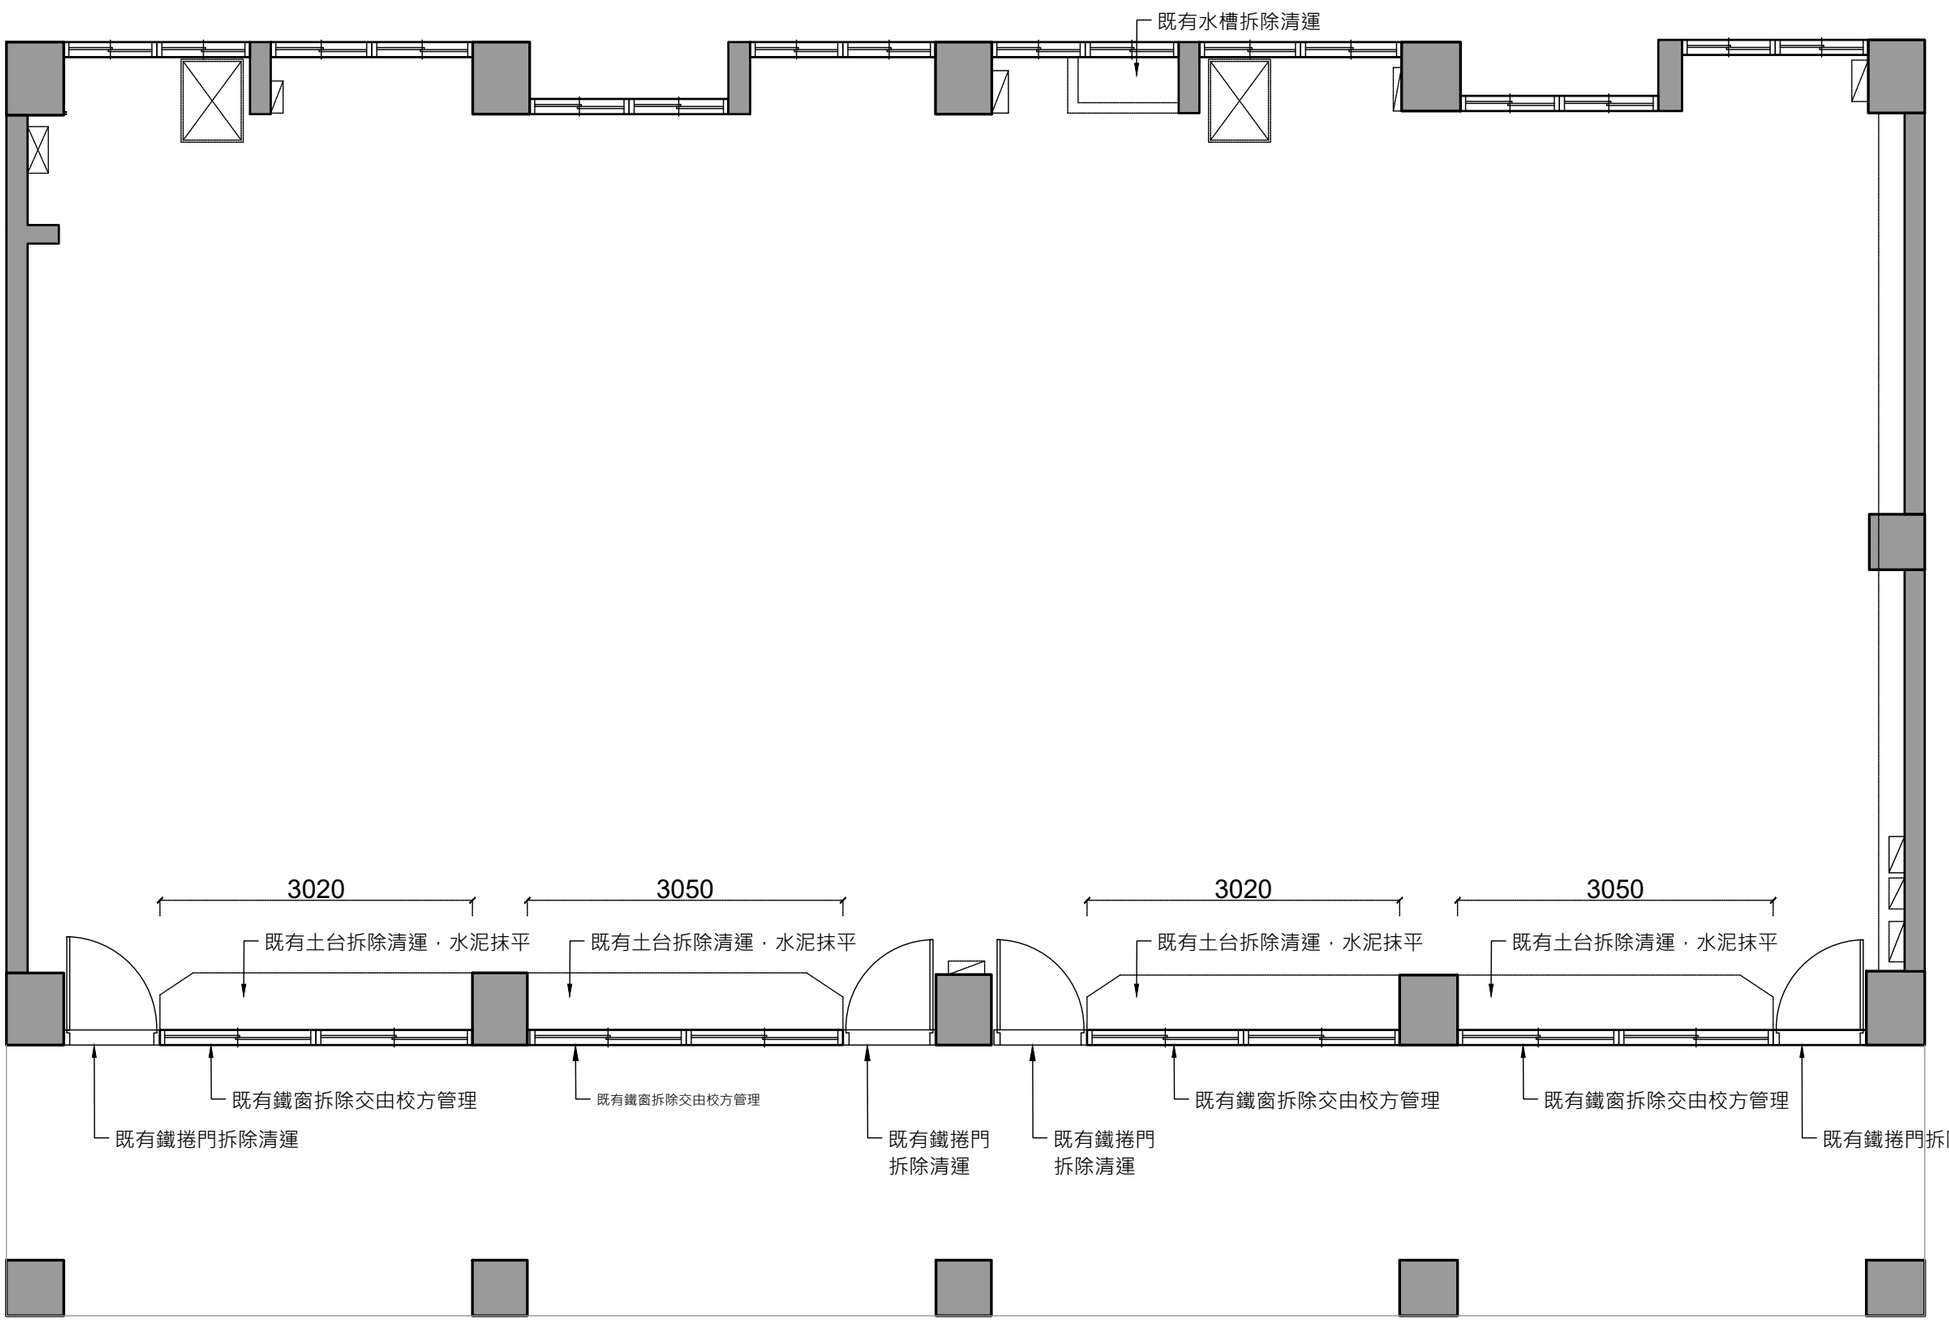

工程名稱 PROJECT

永貞國小圖書館整修工程

圖號 DRAWNG NO.	張號 SHEET NO.
	3/32

圖面修正 REVISISONS

NO.	日期 DATE	內容 REMARKS

圖面名稱 DRAWNGTITLE

現況及結構物拆除示意圖

張薰和建築師事務所
苗栗市國華路158號2樓
電話:037-263019
傳真:037-263851

圖 說 NOTE

起造人及承造人遵守事項

1.起造人於施工前,務請地政機關鑑定界址,
所有尺寸以地政機關鑑界為準,依照實際
基地範圍內配合政府所指定建築線施工,
不得越界侵佔鄰地,更勿擅自先行動工,
否則如有糾紛或受罰,由起造人自行負
法律責任.

2.本設計圖經核准後,起造人及承造人必須
申報開工,按圖施工,並按進度提請竣驗
報告,以備完工時申領使用執照.

3.請切實按核准圖樣施工,如原計劃有未盡
理想之處,欲予變更時,務須事先辦理變
更設計手續,經核准後再行施工,以符法
令,切勿擅自變更,否則其後果由起造人
承造人負全責.

4.建造時屋必須請合法且無欠稅之營造廠
承造.

5.所有基礎,樑柱,樓地板,鋼筋,裝妥
後,請起造人知會建築師簽驗合格後,才
准灌注混凝土.


6.必須注意鄰居房屋之安全,及行人之安全
,並不可將建築物材料堆置於道路上妨礙
交通.

7.房屋完工後,立即拆除工寮,並將房屋用
圍籬路水溝清理修復,然後由承造廠商申
請核發使用執照,再憑使用執照申請接通
水電設備.

8.如有其他臨時發生之疑問,請即提出研討
或向縣市政府建管單位書面查詢,切勿擅
自解釋法令或施做.

9.承造人不得使用下列材料: (1) 海砂
(2) 輻射鋼筋

比例 SCALE	
設計 DESIGN BY	
繪圖 DRAWN BY	
校對 CHECK BY	
核准 APPROVED BY	
日期 DATE	

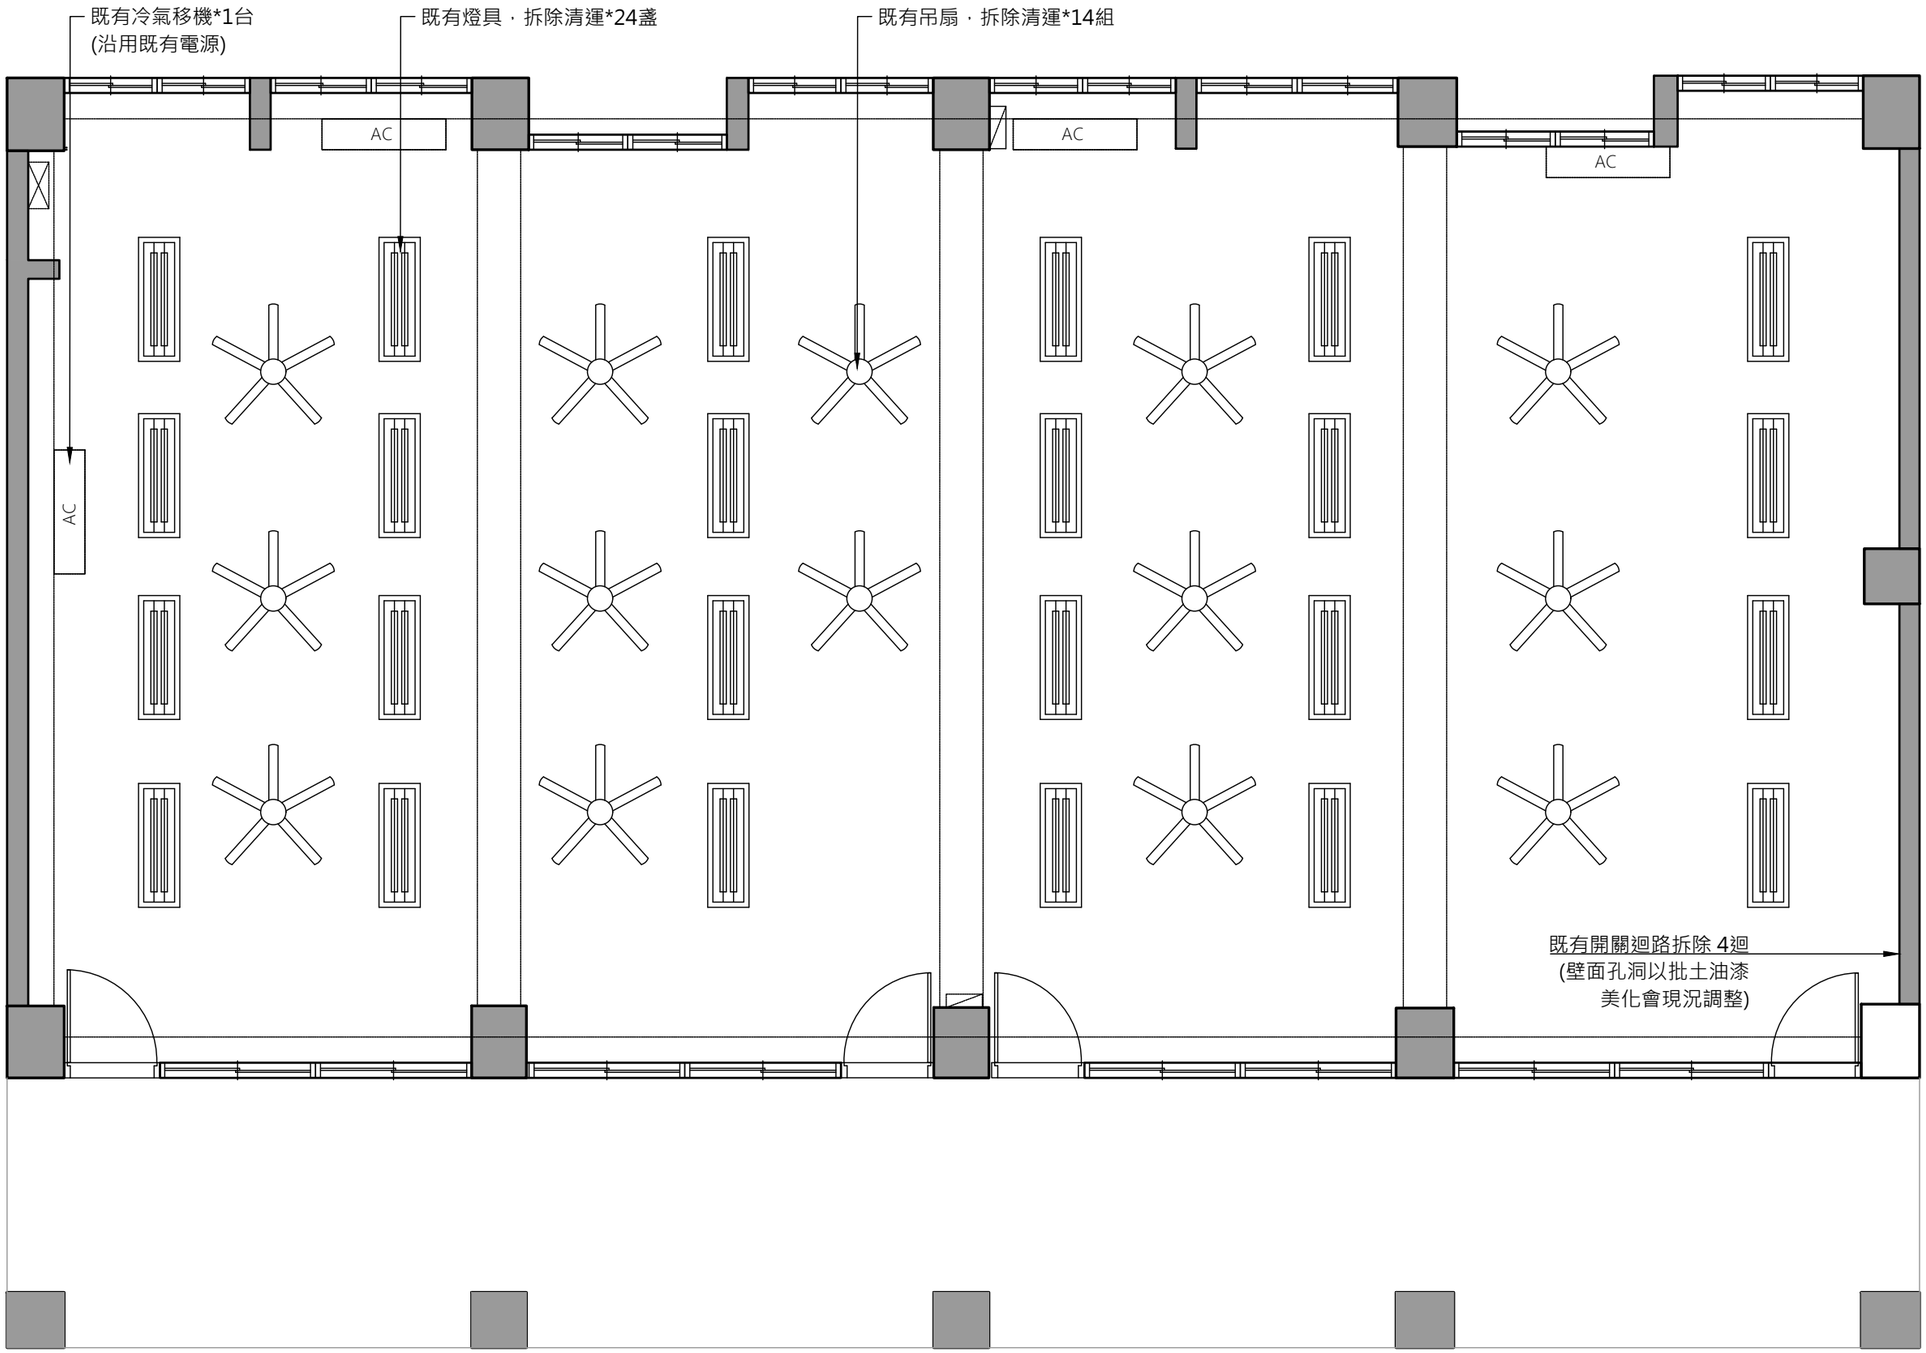

工程名稱 PROJECT

永貞國小圖書館整修工程

圖號 DRAWNG NO.	張號 SHEET NO.
	4/32

圖面修正 REVISISONS

NO.	日期 DATE	內容 REMARKS

圖面名稱 DRAWNGTITLE

既有燈具及電扇拆除示意圖


張薰和建築師事務所
苗栗市國華路158號2樓
電話:037-263019
傳真:037-263851

圖說 NOTE

起造人及承造人遵守事項

1. 起造人於施工前,務請地政機關鑑定界址,所有尺寸以地政機關鑑界為準,依照實際基地範圍內配合政府所指定建築線施工,不得越界侵佔鄰地,要勿擅自先行動工,否則如有糾紛或受罰,由起造人自行負法律責任.
2. 本設計圖經核准後,起造人及承造人必須申報開工,按圖施工,並按進度提請查驗報告,以備完工時申領使用執照.
3. 請切實按核准圖樣施工,如原計劃有未盡理想之處,欲予變更時,務須事先辦理變更設計手續,經核准後再行施工,以符法令,切勿擅自變更,否則其後果由起造人承造人負全責.
4. 建造房屋必須請合法且無欠稅之營造廠承造.
5. 所有基礎,樑柱,樓地板,鋼筋,紮妥後,請起造人知會建築師查驗合格後,才准澆注混凝土.
6. 必須注意鄰居房屋之安全,及行人之安全,並不可將建築物材料堆置於道路上妨礙交通.
7. 房屋完工後,立即拆除工寮,並將房屋周圍道路水溝清理修復,然後由承造廠商申請核發使用執照,再憑使用執照申請接通水電設備.
8. 如有其他臨時發生之疑問,請即提出研討或向縣市政府建管單位書面查詢,切勿擅自解釋法令或施做.
9. 承造人不得使用下列材料:
   (1) 海砂
   (2) 輻射鋼筋

比例 SCALE	
設計 DESIGN BY	
繪圖 DRAWN BY	
校對 CHECK BY	
核准 APPROVED BY	
日期 DATE	

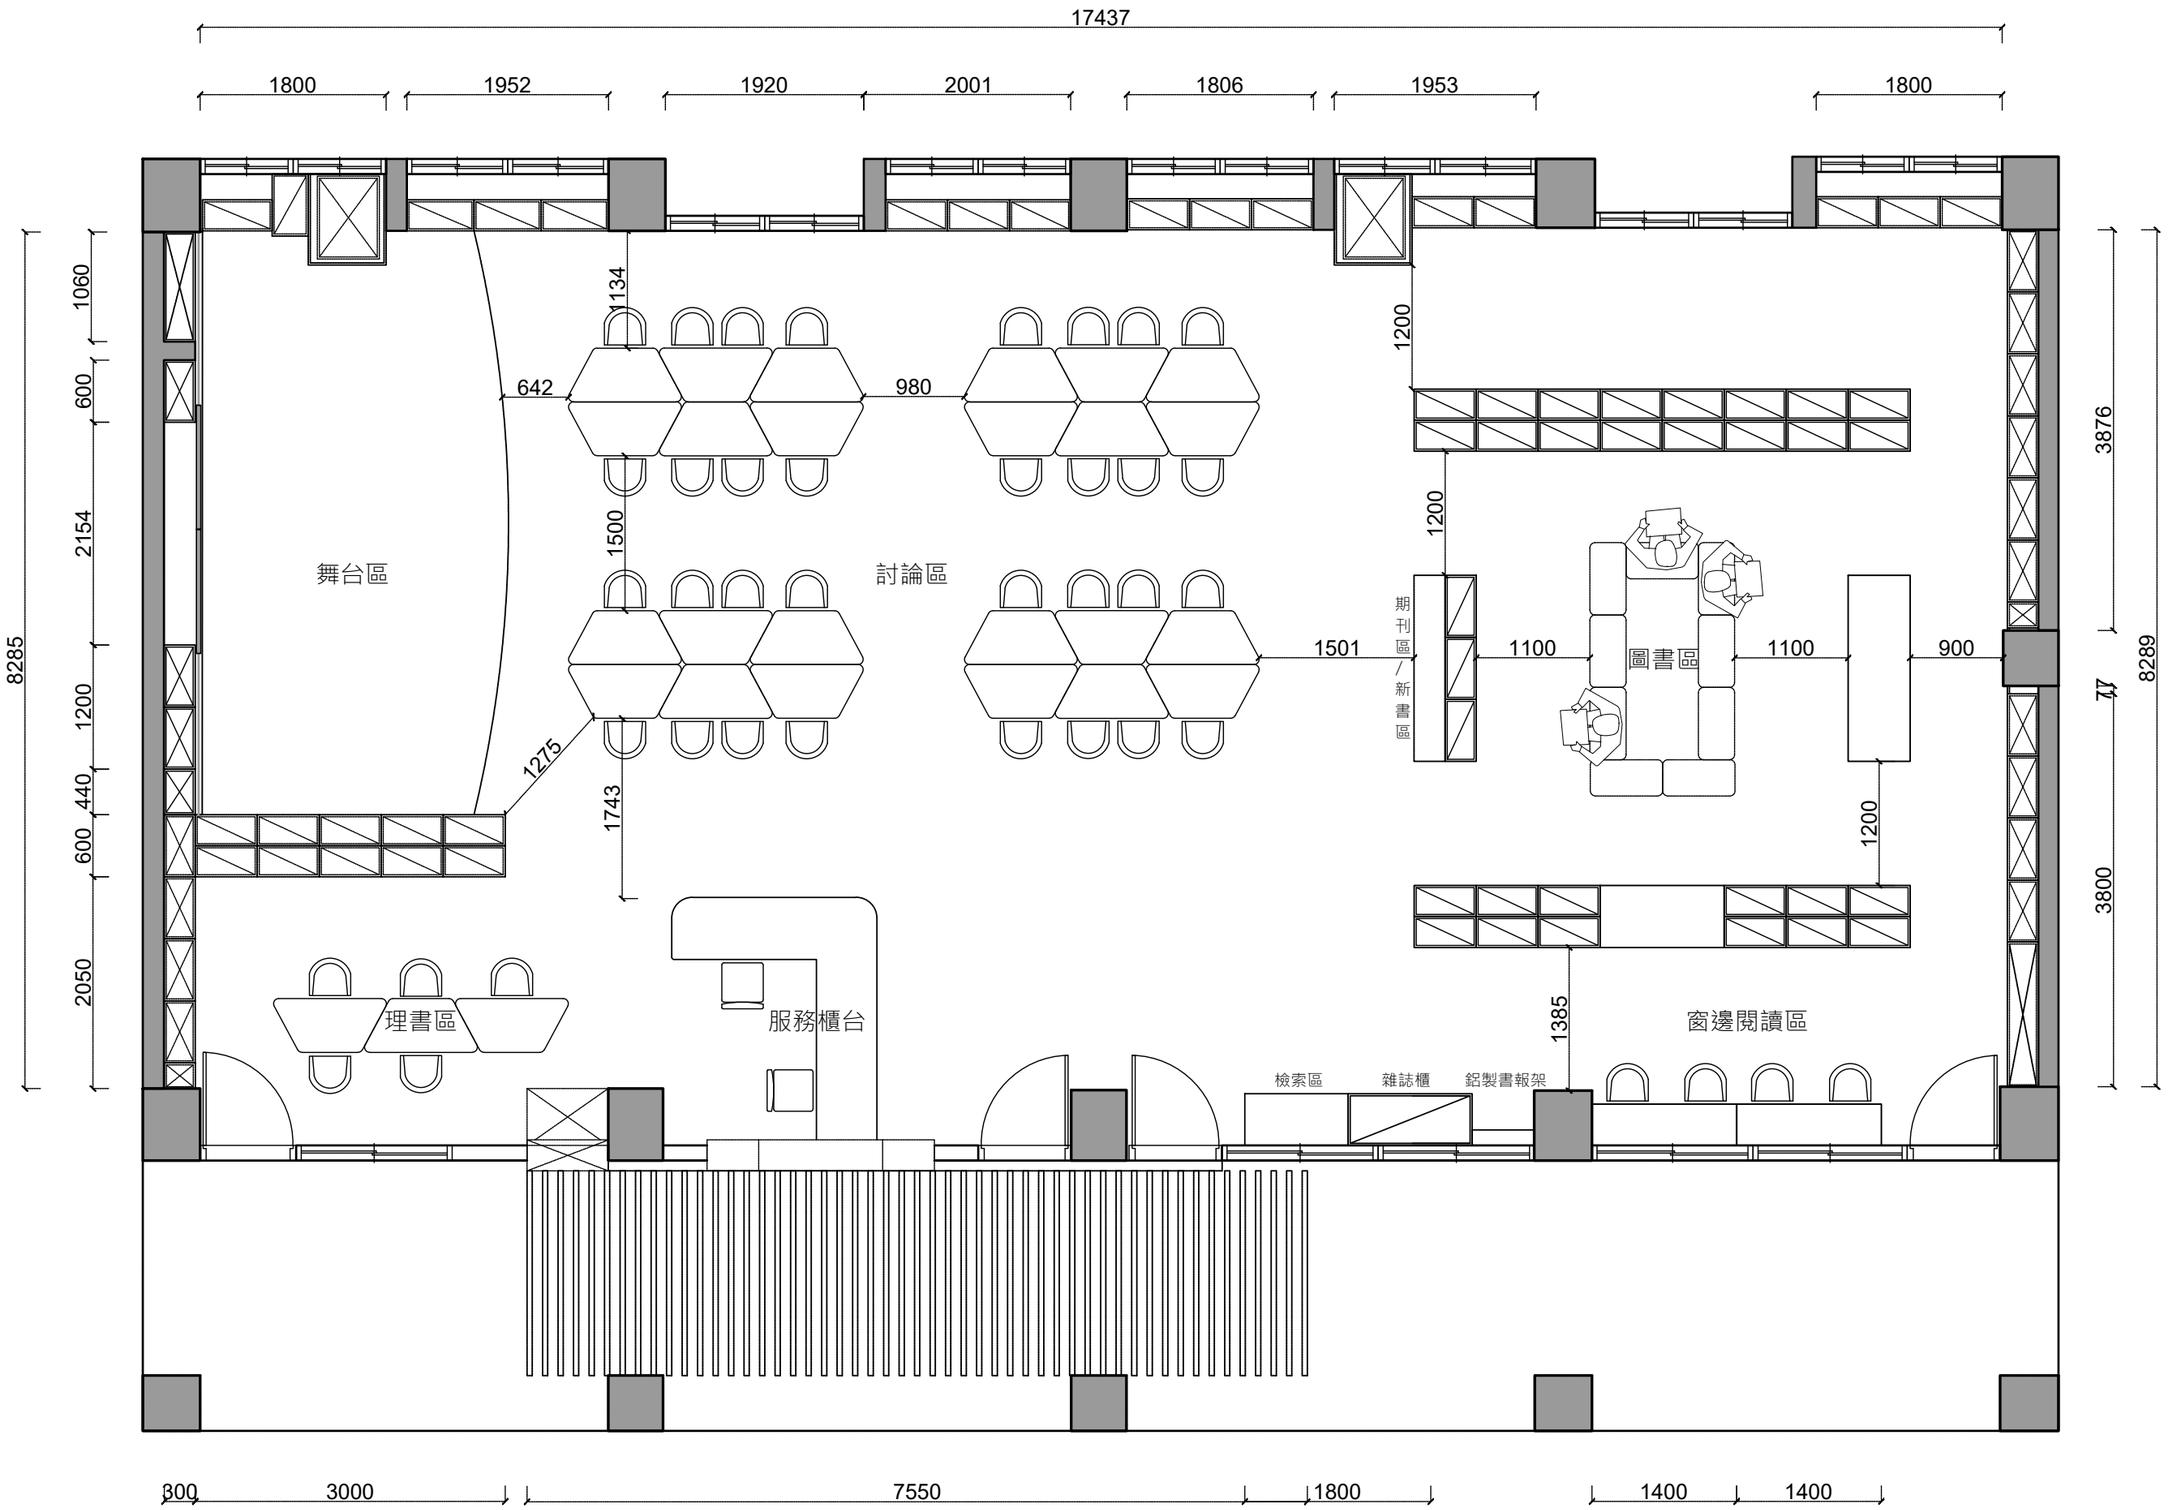

工程名稱 PROJECT

永貞國小圖書館整修工程

圖號 DRAWNG NO.	張號 SHEET NO.
	5/32

圖面修正 REVISISONS

NO.	日期 DATE	內容 REMARKS

圖面名稱 DRAWNGTITLE

平面配置圖

張薰和建築師事務所

苗栗市國華路158號2樓

電話:037-263019

傳真:037-263851

圖 說 NOTE

起造人及承造人遵守事項

1.起造人於施工前,務請地政機關鑑定界址,所有尺寸以地政機關鑑界為準,依照實際基地範圍內配合政府所指定建照線施工,不得越界侵佔鄰地,要勿擅自先行動工,否則如有糾紛或受罰,由起造人自行負法律責任.

2.本設計圖經核准後,起造人及承造人必須申報開工,按圖施工,並按進度提請查驗報告,以俾完工時申領使用執照.

3.請切實按核准圖樣施工,如原計劃有未盡理想之處,欲予變更時,務須事先辦理變更設計手續,經核准後再行施工,以符法令,切勿擅自變更,否則其後果由起造人承造人負全責.

4.建造房屋必須請合法且無欠稅之營造廠承造.

5.所有基礎,樑柱,樓地板,鋼筋,紮妥後,請起造人知會建築師前來驗合格後,才澆灌注混凝土.


6.必須注意鄰居房屋之安全,及行人之安全,並不可將建築物材料堆置於道路上妨礙交通.

7.房屋完工後,立即拆除工寮,並將房屋周圍道路水溝清理修復,然後由承造廠商申請核發使用執照,再憑使用執照申請接通水電設備.

8.如有其他臨時發生之疑問,請即提出研討或向轄市政府建管單位書面查詢,切勿擅自解釋法令或臆揣.

9.承造人不得使用下列材料: (1) 海砂
(2) 輻射鋼筋

比例 SCALE	
設計 DESIGN BY	
繪圖 DRAWN BY	
校對 CHECK BY	
核准 APPROVED BY	
日期 DATE	

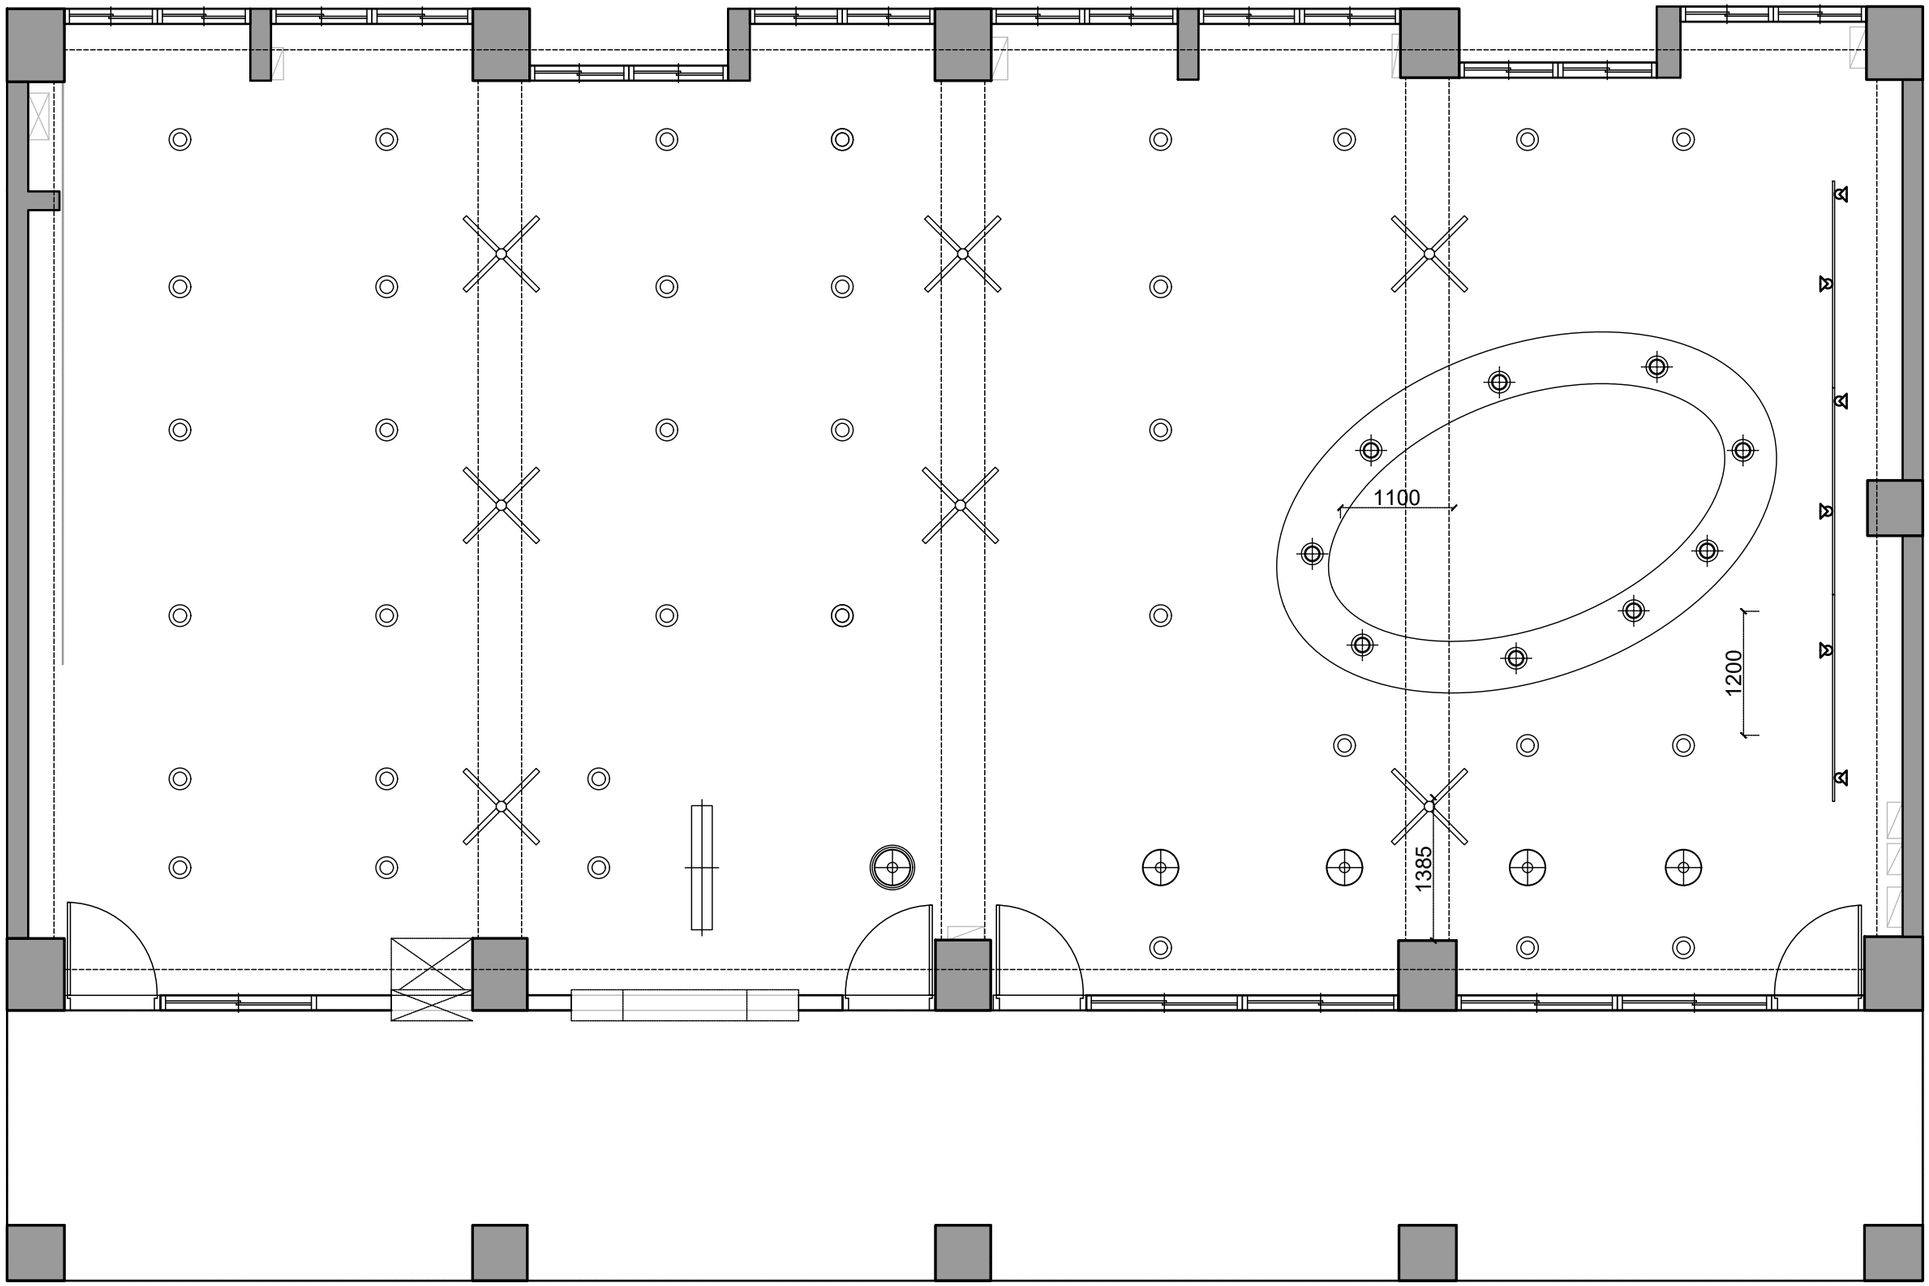

名稱	圖示	數量	名稱	圖示	數量	名稱	圖示	數量	名稱	圖示	數量	名稱	圖示	數量
藤編吊燈(小)		4組	吸頂式筒燈		35組	2米軌道 散光投射組		3組	LED吊燈組		1組	LED公分崁燈		9組
名稱	圖示	數量	名稱	圖示	數量									
藤編吊燈(大)		1組	吊扇		7組									

工程名稱 PROJECT

永貞國小圖書館整修工程

圖號 DRAWNG NO.	張號 SHEET NO.
	6/32

圖面修正 REVISISONS

NO.	日期 DATE	內容 REMARKS

圖面名稱 DRAWNGTITLE

新設燈具配置圖(一)


張薰和建築師事務所
苗栗市國華路158號2樓
電話:037-263019
傳真:037-263851

圖 說 NOTE

起造人及承造人遵守事項

1.起造人於施工前,務請地政機關鑑定界址,所有尺寸以地政機關鑑界為準,免照實際基地範圍內配合政府所指定建築線施工,不得越界侵佔鄰地,更勿擅自先行動工,否則所有糾紛或受罰,由起造人自行負法律責任.
2.本設計圖經核准後,起造人及承造人必須申報開工,按圖施工,並按進度提請查驗報告,以備完工時申領使用執照.
3.請切實按核准圖樣施工,如原計劃有未盡理想之處,欲予變更時,務須事先辦理變更設計手續,經核准後再行施工,以符法令,切勿擅自變更,否則其後果由起造人承造人負全責.
4.建築房屋必須請合法且無欠稅之營造廠承造.
5.所有基礎,樑柱,樓地板,鋼筋,紮妥後,請起造人知會建築師查驗合格後,才准灌注混凝土.
6.必須注意鄰居房屋之安全,及行人之安全,並不可將建築物材料堆置於道路上妨礙交通.
7.房屋完工後,立即拆除工寮,並將房屋周圍道路水溝清理修復,然後由承造廠商申請核發使用執照,再憑使用執照申請接通水電設備.
8.如有其他臨時發生之疑問,請即提出研討或向縣市政府建管單位書面查詢,切勿擅自解釋法令或施做.
9.承造人不得使用下列材料: (1) 海砂 (2) 輻射鋼筋

比例 SCALE	
設計 DESIGN BY	
繪圖 DRAWN BY	
校對 CHECK BY	
核准 APPROVED BY	
日期 DATE	

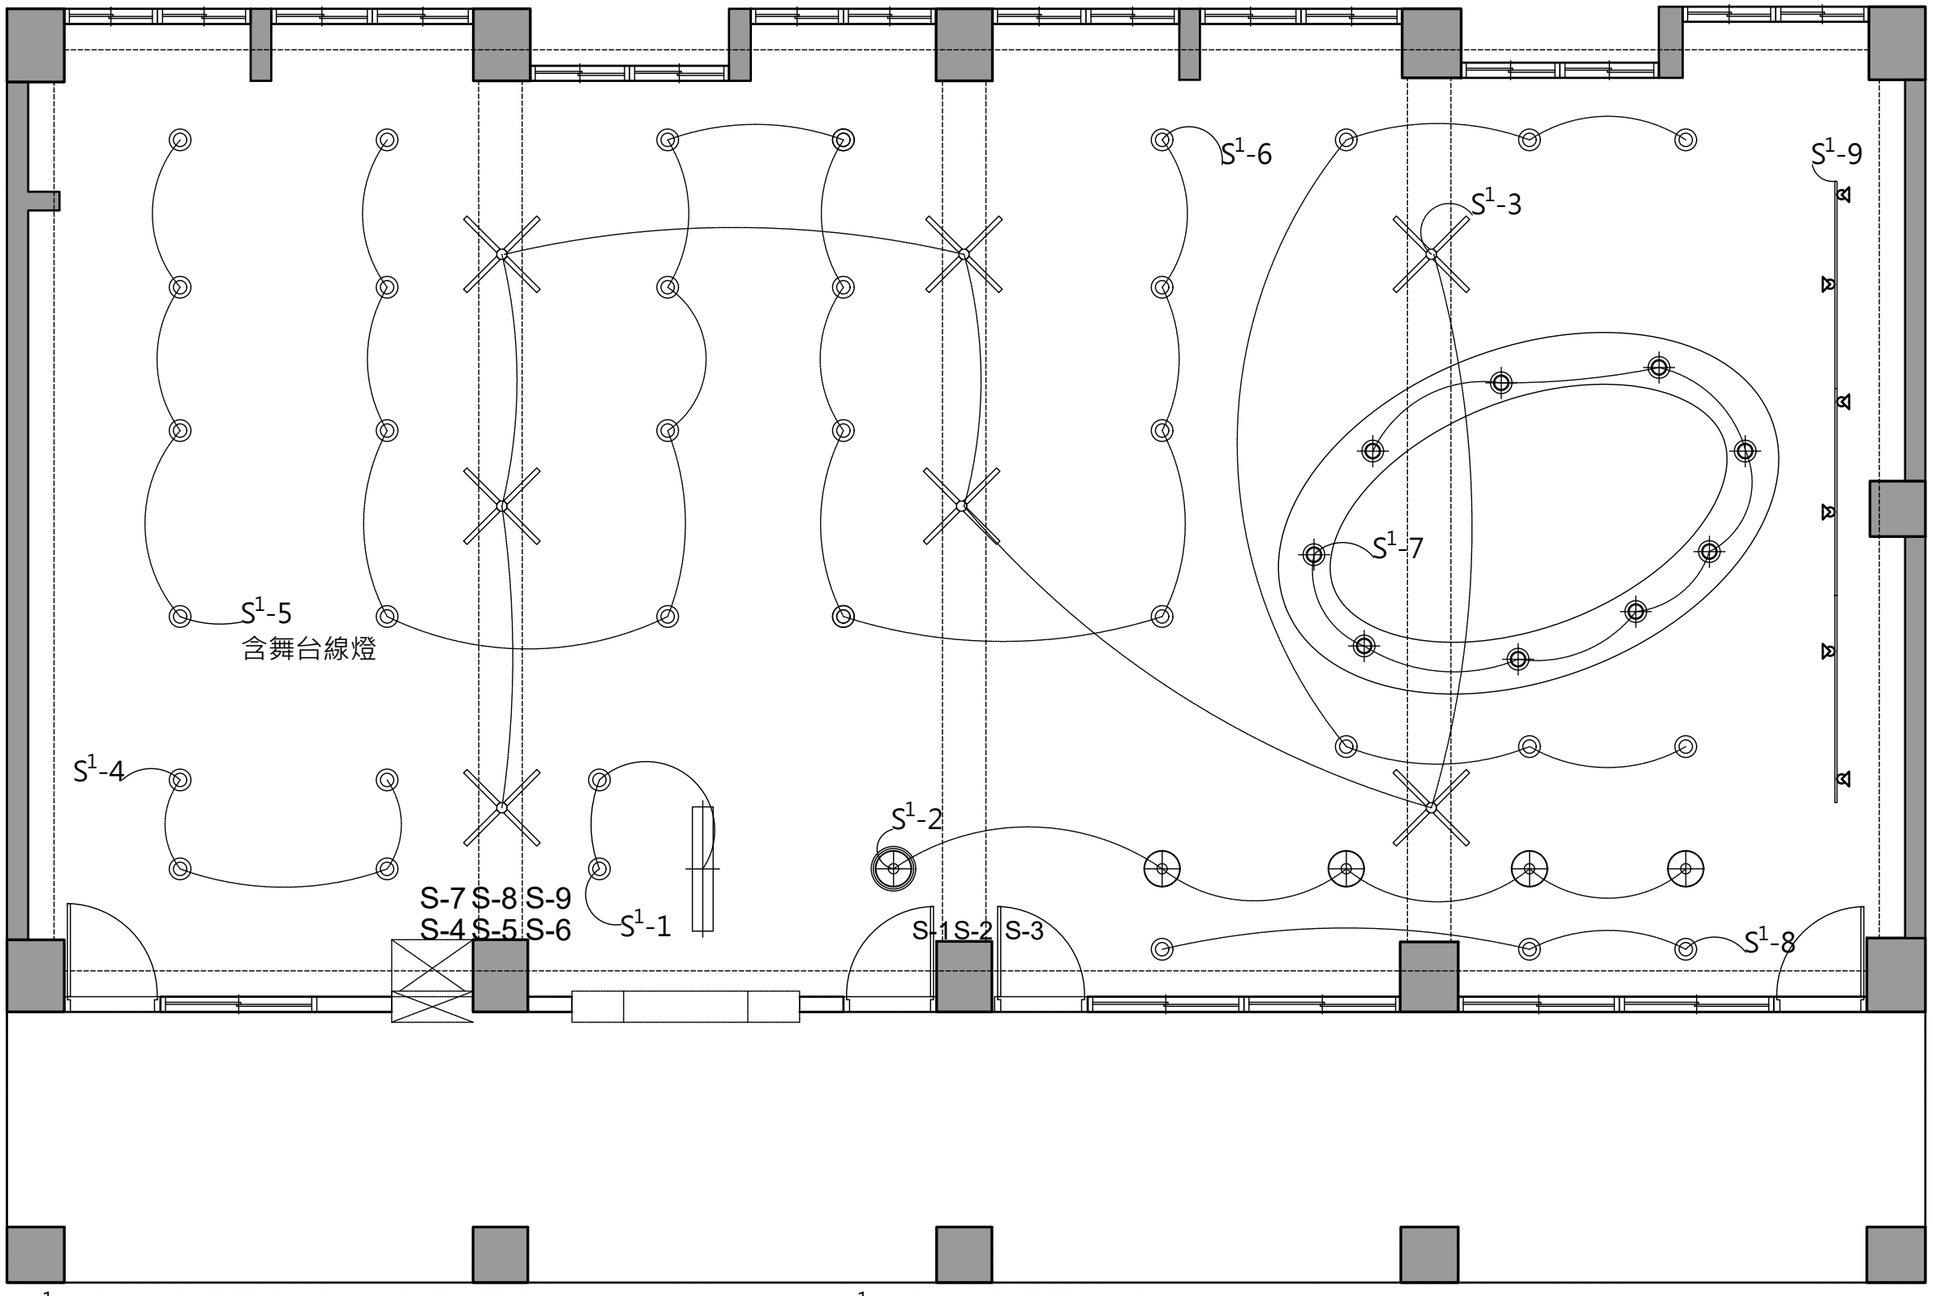

S^1-1-附載2組"吸頂式筒燈"+1組"日光吊燈"
S^1-2-附載5組"藤編吊燈(大)*1組+藤扁吊燈(小)*4組"
S^1-3-附載7組"吊扇"
S^1-4-附載4組"吸頂式筒燈"
S^1-5-附載5組"吸頂式筒燈"*4組+"LED線燈"*1組
S^1-6-附載16組"吸頂式筒燈"
S^1-7-附載9組"LED崁燈"
S^1-8-附載3組"吸頂式筒燈"
S^1-9-附載6組"軌道燈"

工程名稱 PROJECT

永貞國小圖書館整修工程

圖號 DRAWNG NO.	張號 SHEET NO.
	7/32

圖面修正 REVISISONS

NO.	日期 DATE	內容 REMARKS

圖面名稱 DRAWNGTITLE

新設燈具迴路圖

張薰和建築師事務所
苗栗市國華路158號2樓
電話:037-263019
傳真:037-263851

圖 說 NOTE

起造人及承造人遵守事項

1.起造人於施工前,務請地政機關鑑定界址,所有尺寸以地政機關鑑界為準,依照實際基地範圍內配合政府所指定建築線施工,不得越界侵佔鄰地,更勿擅自先行動工,否則如有糾紛或受罰,由起造人自行負法律責任.

2.本設計圖經核准後,起造人及承造人必須申報開工,按圖施工,並按進度提請查驗報告,以備完工時申領使用執照.

3.請切實按核准圖樣施工,如原計劃有未盡理想之處,欲予變更時,務須事先辦理變更設計手續,經核准後再行施工,以符法令,切勿擅自變更,否則其後果由起造人承造人負全責.

4.建築房屋必須請合法且無欠稅之營造廠承造.

5.所有基礎,樑柱,樓地板,鋼筋紮妥後,請起造人知會建築師查驗合格後,才准灌注混凝土.


6.必須注意鄰居房屋之安全,及行人之安全,並不可將建築物材料堆置於道路上妨礙交通.

7.房屋完工後,立即拆除工寮,並將房屋周圍道路水溝清理修復,然後由承造廠商申請核發使用執照,再憑使用執照申請接通水電設備.

8.如有其他臨時發生之疑問,請即提出研討或向縣市政府建管單位書面咨詢,切勿擅自解釋法令或施做.

9.承造人不得使用下列材料: (1) 海砂 (2) 輻射鋼筋

比例 SCALE	
設計 DESIGN BY	
繪圖 DRAWN BY	
校對 CHECK BY	
核准 APPROVED BY	
日期 DATE	

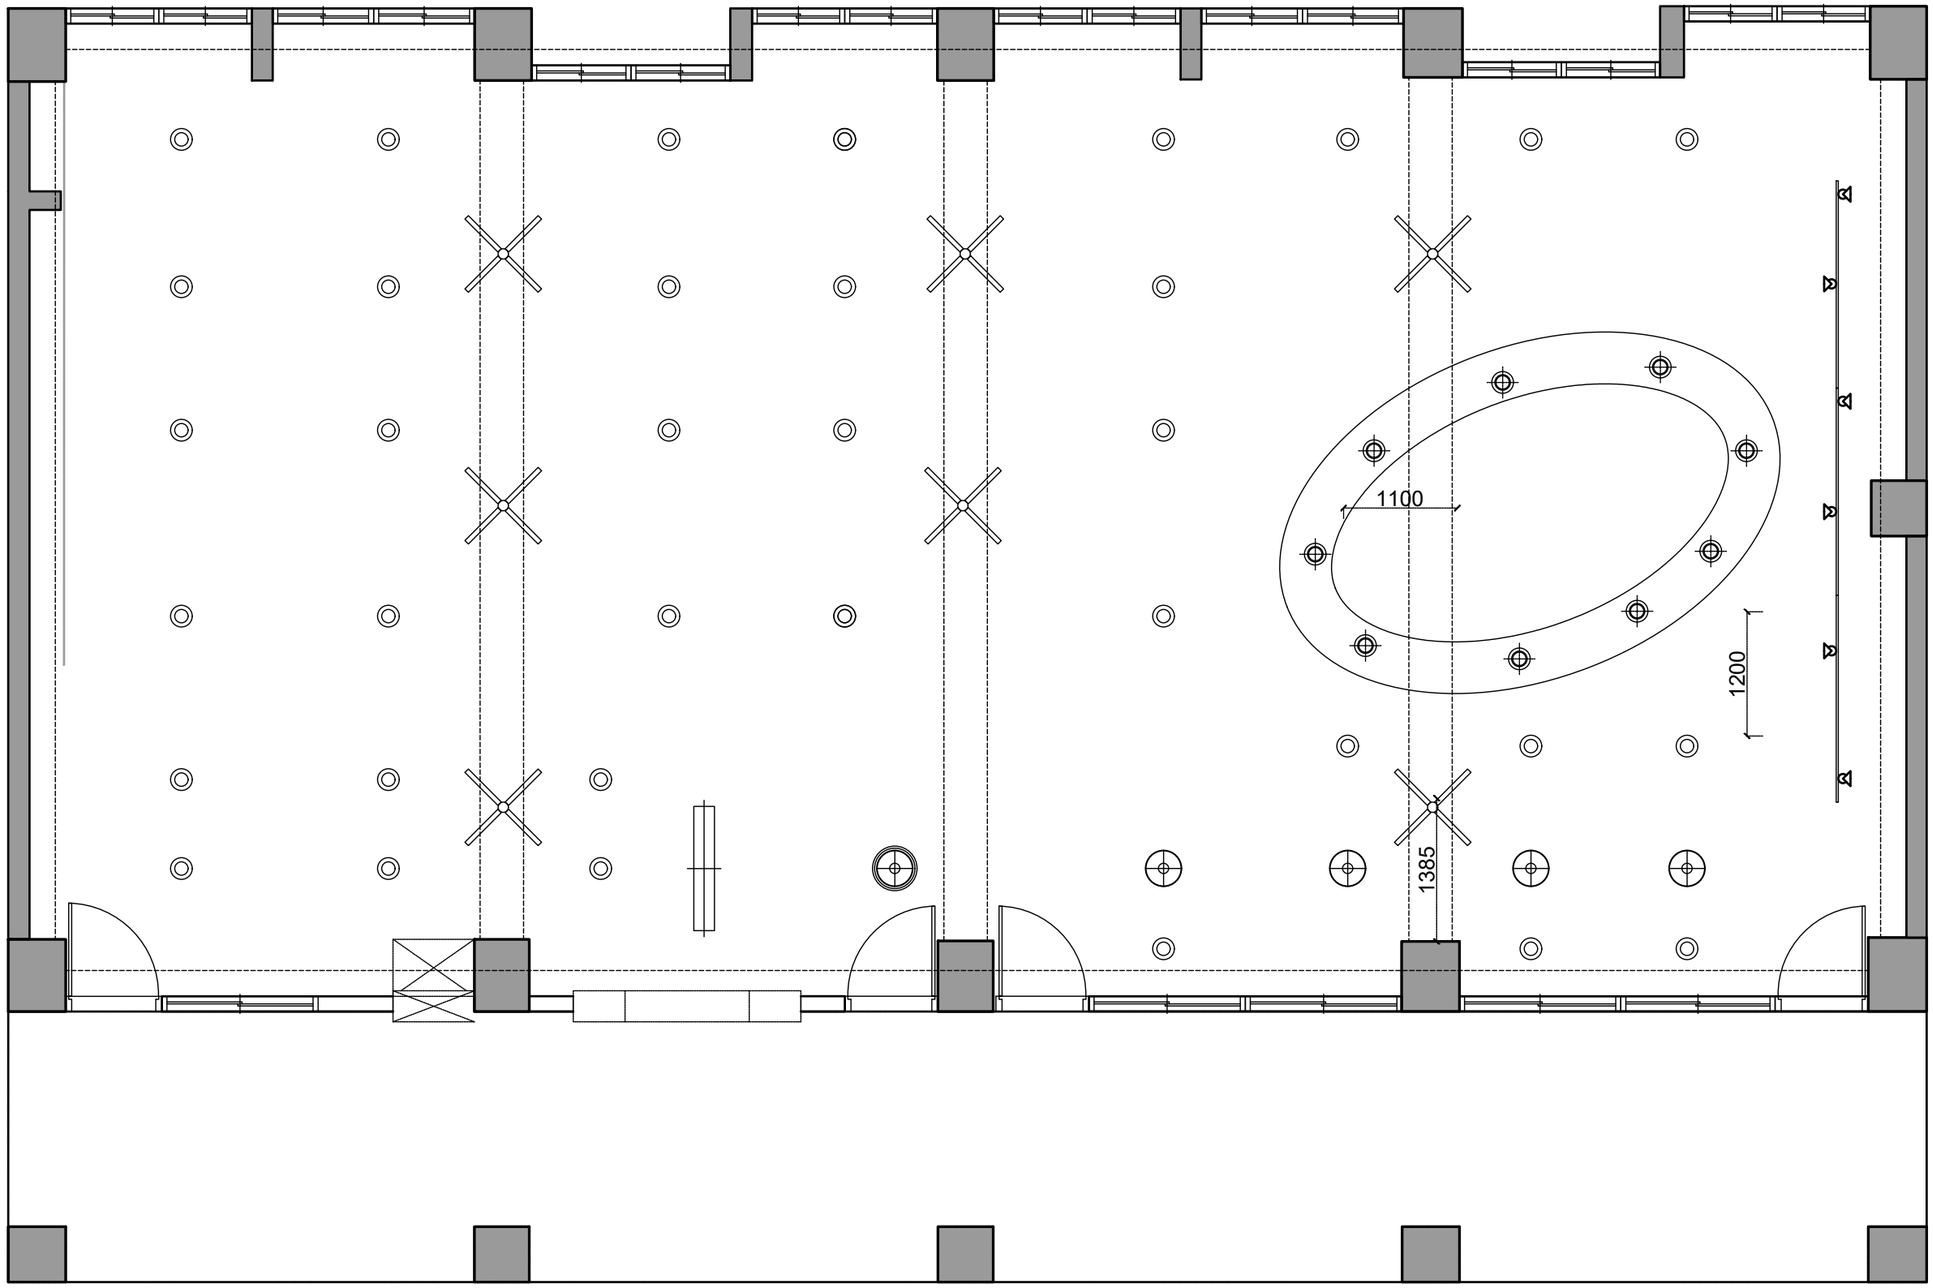

藤編吊燈	E27燈泡 16W 2000ml	5盞*2000ml=10000ml
吸頂式筒燈	20W 2450ml	35盞*2450ml=85750ml
聚光型軌道燈	14W 1150ml	6盞*1150ml=6900ml
LED崁燈	16W 1520ml	9盞*1150ml=13680ml

總照度計算式=總流明數/總M^2
10000+85750+6900+13680=116330

Lux=116330/167M^2=696Lus
(平均照度參考數據)

工程名稱 PROJECT

永貞國小圖書館整修工程

圖號 DRAWNG NO.	張號 SHEET NO.
	8/32

圖面修正 REVISISONS

NO.	日期 DATE	內容 REMARKS

圖面名稱 DRAWNGTITLE

新設燈具配置圖(照圖分析圖)


張薰和建築師事務所
苗栗市國華路158號2樓
電話:037-263019
傳真:037-263851

圖 說 NOTE

起造人及承造人遵守事項

1.起造人於施工前,務請地政機關鑑定界址,所有尺寸以地政機關鑑界為準,依照實際基地範圍內配合政府所指定建築線施工,不得越界侵佔鄰地,更勿擅自先行動工,否則如有糾紛或受罰,由起造人自行負法律責任。
2.本設計圖經核准後,起造人及承造人必須申報開工,按圖施工,並按進度提請查驗報告,以備完工時申領使用執照。
3.請切實按核准圖樣施工,如原計劃有未盡理想之處,欲予變更時,務須事先辦理變更設計手續,經核准後再行施工,以符法令,切勿擅自變更,否則其後果由起造人承造人負全責。
4.建築基地必須請合法且無欠稅之營造廠承造。
5.所有基礎,樑柱,樓地板,鋼筋,紮妥後,請起造人知會建築師查驗合格後,才准灌注混凝土。
6.必須注意鄰居房屋之安全,及行人之安全,並不可將建築物材料堆置於道路上妨礙交通。
7.房屋完工後,立即拆除工寮,並將房屋周圍排水溝清理修復,然後由承造廠商申請核發使用執照,再憑使用執照申請接通水電設備。
8.如有其他臨時發生之疑問,請即提出研討或向縣市政府建管單位書面查詢,切勿擅自解釋法令或施做。
9.承造人不得使用下列材料: (1) 海砂 (2) 輻射鋼筋

比例 SCALE	
設計 DESIGN BY	
繪圖 DRAWN BY	
校對 CHECK BY	
核准 APPROVED BY	
日期 DATE	

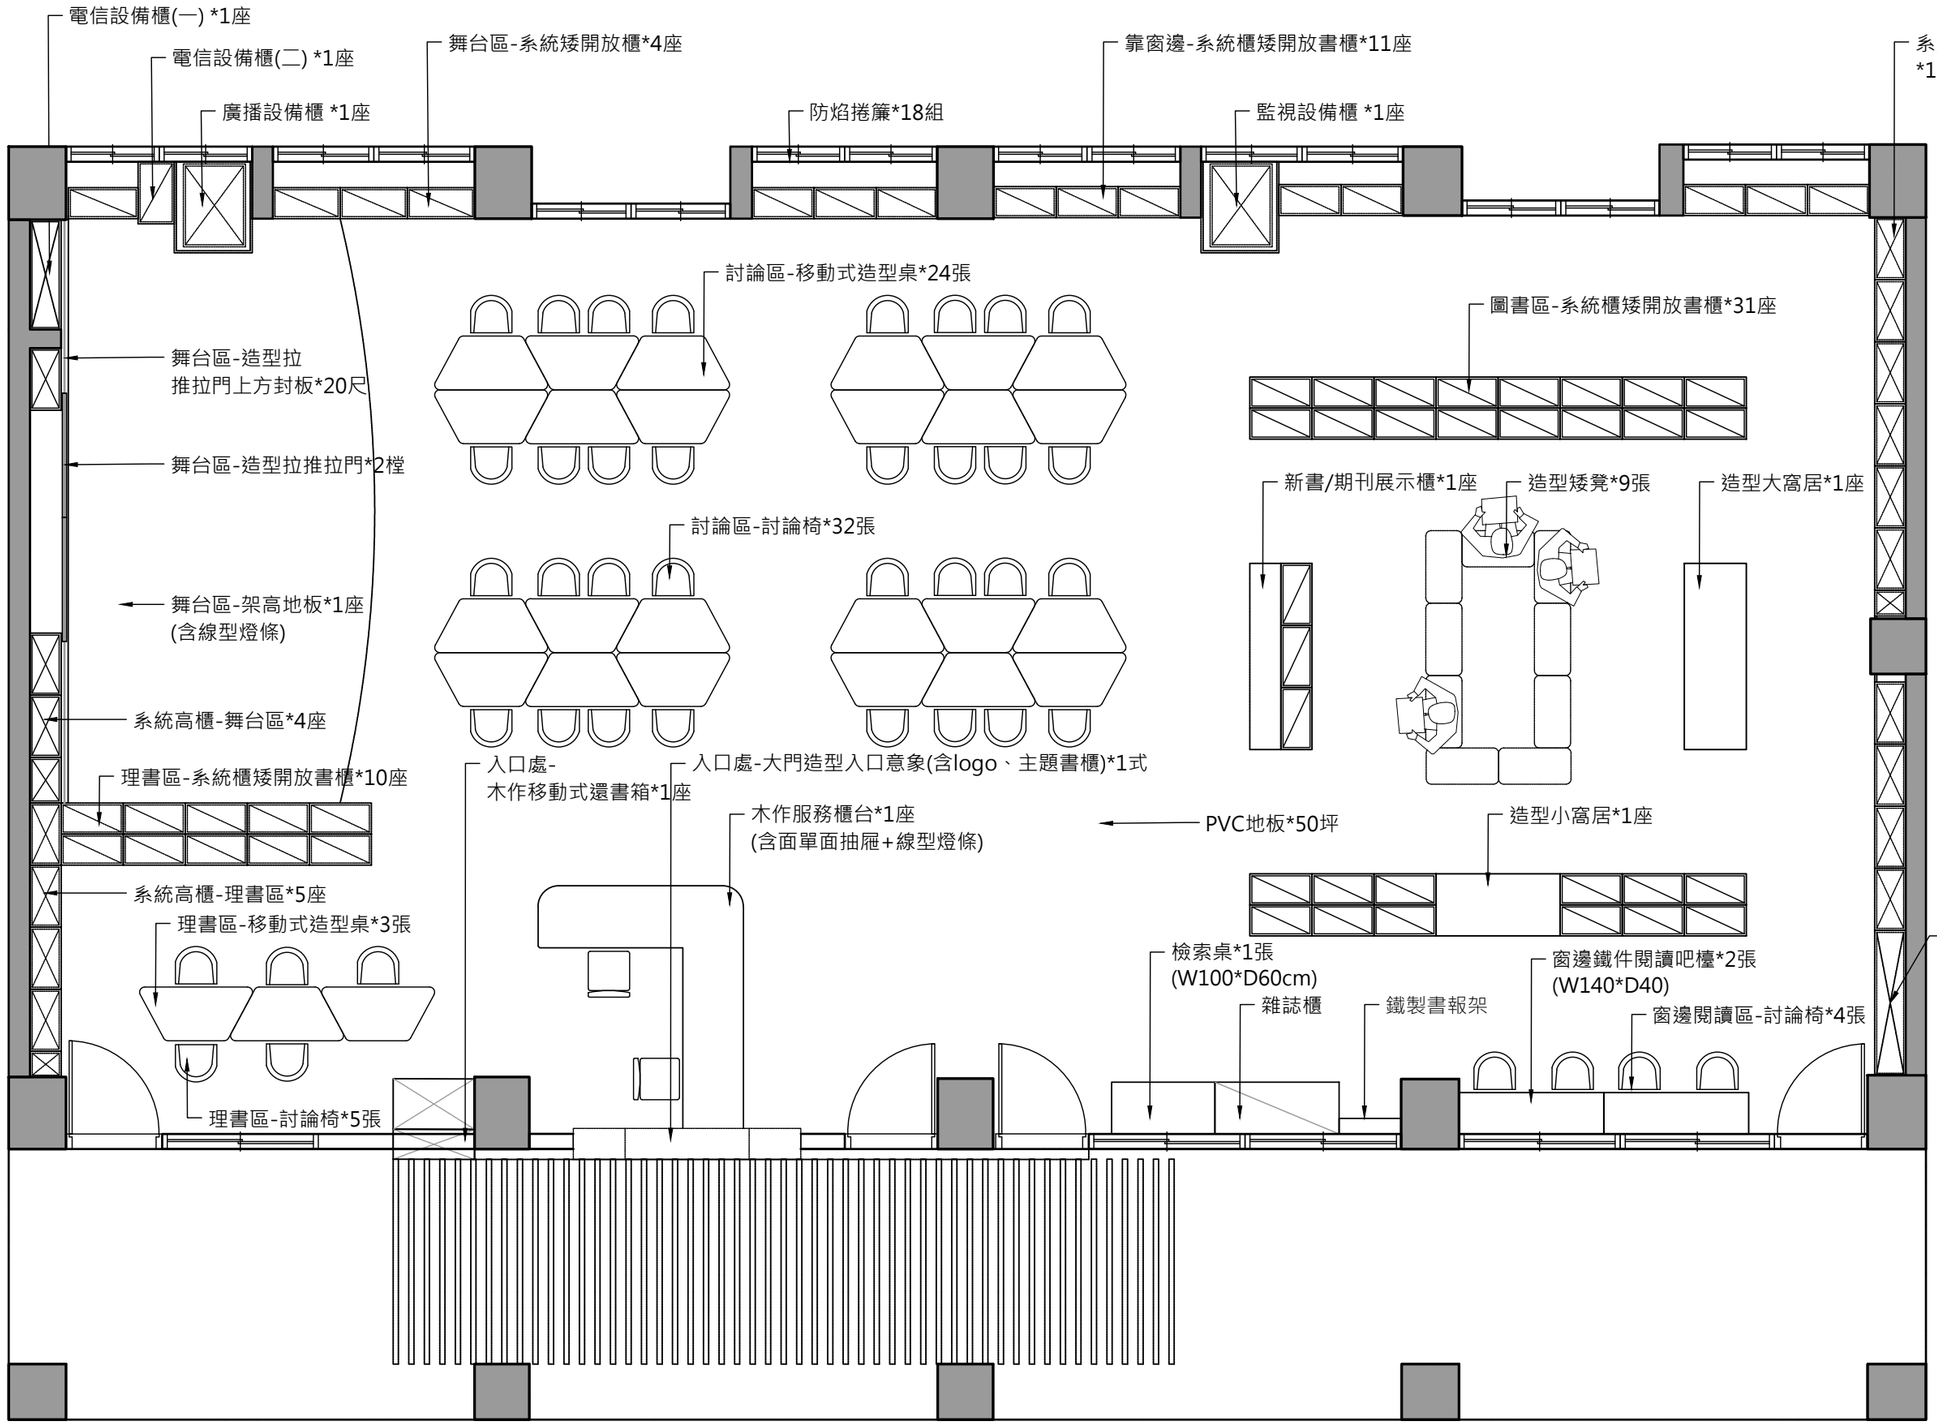

工程名稱 PROJECT

永貞國小圖書館整修工程

圖號 DRAWNG NO.	張號 SHEET NO.
	9/32

圖面修正 REVISISONS

NO.	日期 DATE	內容 REMARKS

圖面名稱 DRAWNGTITLE

平面配置圖(二)

張薰和建築師事務所
苗栗市國華路158號2樓
電話:037-263019
傳真:037-263851

圖 說 NOTE

起造人及承造人遵守事項

1.起造人於施工前,務請地政機關鑑定界址,所有尺寸以地政機關鑑界為準,依照實際基地範圍內配合政府所指定建築線施工,不得越界侵佔鄰地,更勿擅自先行動工,否則需有糾紛或受罰,由起造人自行負法律責任。

2.本設計圖經核准後,起造人及承造人必須申報開工,按圖施工,並按進度提請查驗報告,以備完工時申領使用執照。

3.請切實按核准圖樣施工,如原計劃有未盡理想之處,欲予變更時,務須事先辦理變更設計手續,經核准後再行施工,以符法令,切勿擅自變更,否則其後果由起造人承造人負全責。

4.建築師見習必須請合法且無欠稅之營造廠承造。

5.所有基礎,樑柱,樓地板,鋼筋,紮妥後,請起造人知會建築師簽驗合格後,才准灌注混凝土。


6.必須注意鄰居房屋之安全,及行人之安全,並不可將建築物材料堆置於道路上妨礙交通。

7.房屋完工後,立即拆除工寮,並將房屋周圍園路水溝清理修復,然後由承造廠商申請核發使用執照,再憑使用執照申請接通水電設備。

8.如有其他臨時發生之疑問,請即提出研討或向縣市政府建管單位書面查詢,切勿擅自解釋法令或施做。

9.承造人不得使用下列材料: (1) 海砂
(2) 輻射鋼筋

比例 SCALE	
設計 DESIGN BY	
繪圖 DRAWN BY	
校對 CHECK BY	
核准 APPROVED BY	
日期 DATE	

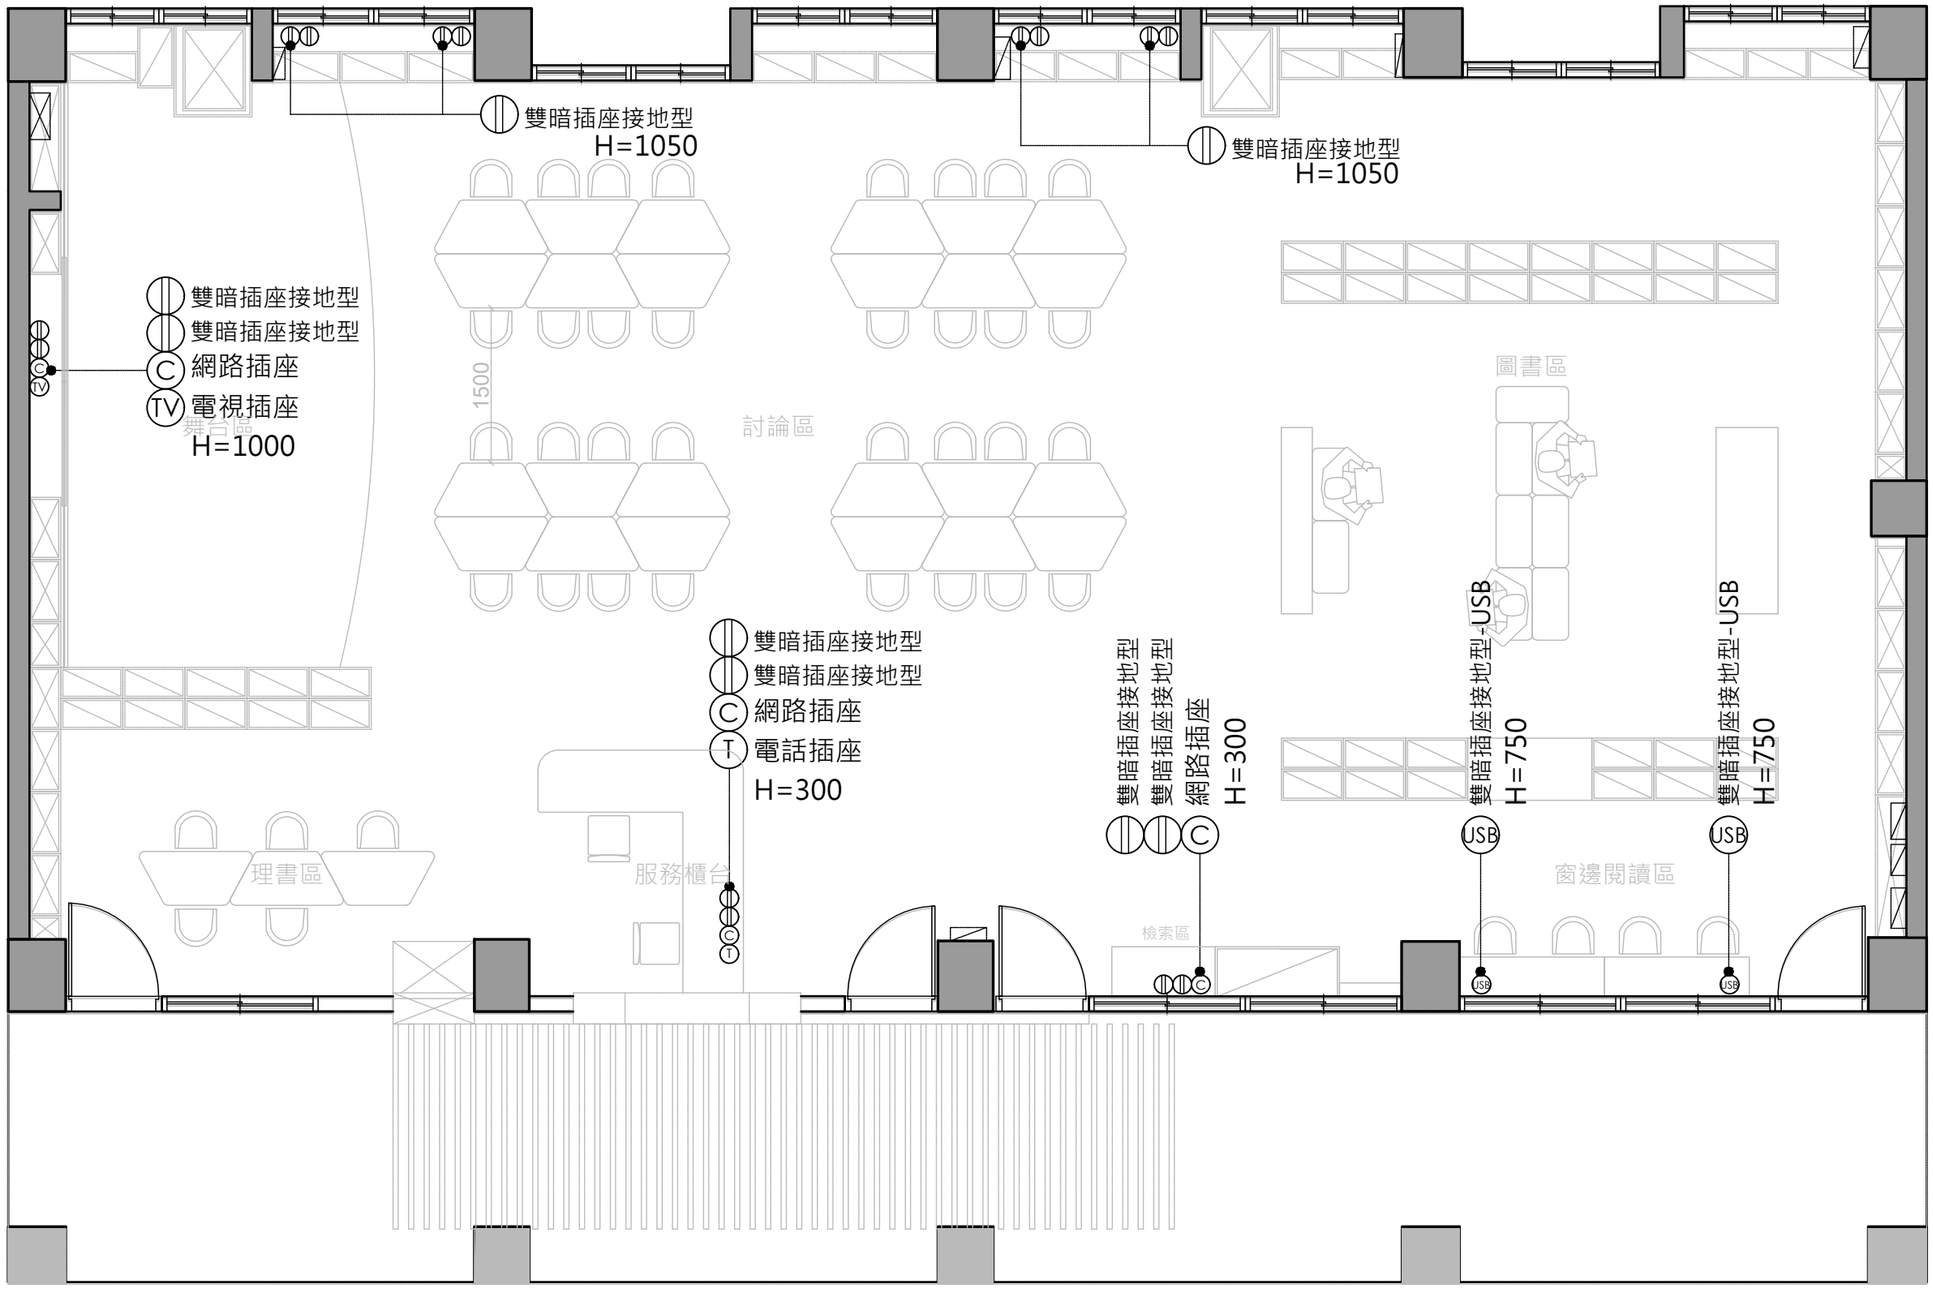

圖示	說明	數量
◍	雙暗插座接地型	14迴
Ⓒ	網路插座	3迴
USB	雙暗插座接地型-USB	2迴
Ⓣ	電話插座	1迴
TV	電視插座	1迴

工程名稱 PROJECT

永貞國小圖書館整修工程

圖號 DRAWNG NO.	張號 SHEET NO.
	10/32

圖面修正 REVISISONS

NO.	日期 DATE	內容 REMARKS

圖面名稱 DRAWNGTITLE

新設電源網路配置圖


張薰和建築師事務所
苗栗市國華路158號2樓
電話:037-263019
傳真:037-263851

圖 說 NOTE

起造人及承造人遵守事項

1.起造人於施工前,務請地政機關鑑定界址,所有尺寸以地政機關鑑界為準,免照實際基地範圍內配合政府所指定建築線施工,不得越界侵佔鄰地,更勿擅自先行動工,否則所有糾紛或受損,由起造人自行負法律責任.
2.本設計圖經核准後,起造人及承造人必須申報開工,按圖施工,並按進度提請查驗報告,以備完工時申領使用執照.
3.請切實按核准圖樣施工,如原計劃有未盡理想之處,欲予變更時,務須事先辦理變更設計手續,經核准後再行施工,以符法令,切勿擅自變更,否則其後果由起造人承造人負全責.
4.建造房屋必須請合法且無欠稅之營造廠承造.
5.所有基礎,樑柱,樓地板,鋼筋,紮妥後,請起造人知會建築師簽驗合格後,才准灌注混凝土.
6.必須注意鄰居房屋之安全,及行人之安全,並不可將建築物材料堆置於道路上妨礙交通.
7.房屋完工後,立即拆除工寮,並將房屋周圍道路水溝清理修復,然後由承造廠商申請核發使用執照,再憑使用執照申請接通水電設備.
8.如有其他臨時發生之疑問,請即提出研討或向縣市政府建管單位書面查詢,切勿擅自解釋法令或施做.
9.承造人不得使用下列材料: (1) 海砂 (2) 輻射鋼筋

比例 SCALE	
設計 DESIGN BY	
繪圖 DRAWN BY	
校對 CHECK BY	
核准 APPROVED BY	
日期 DATE	

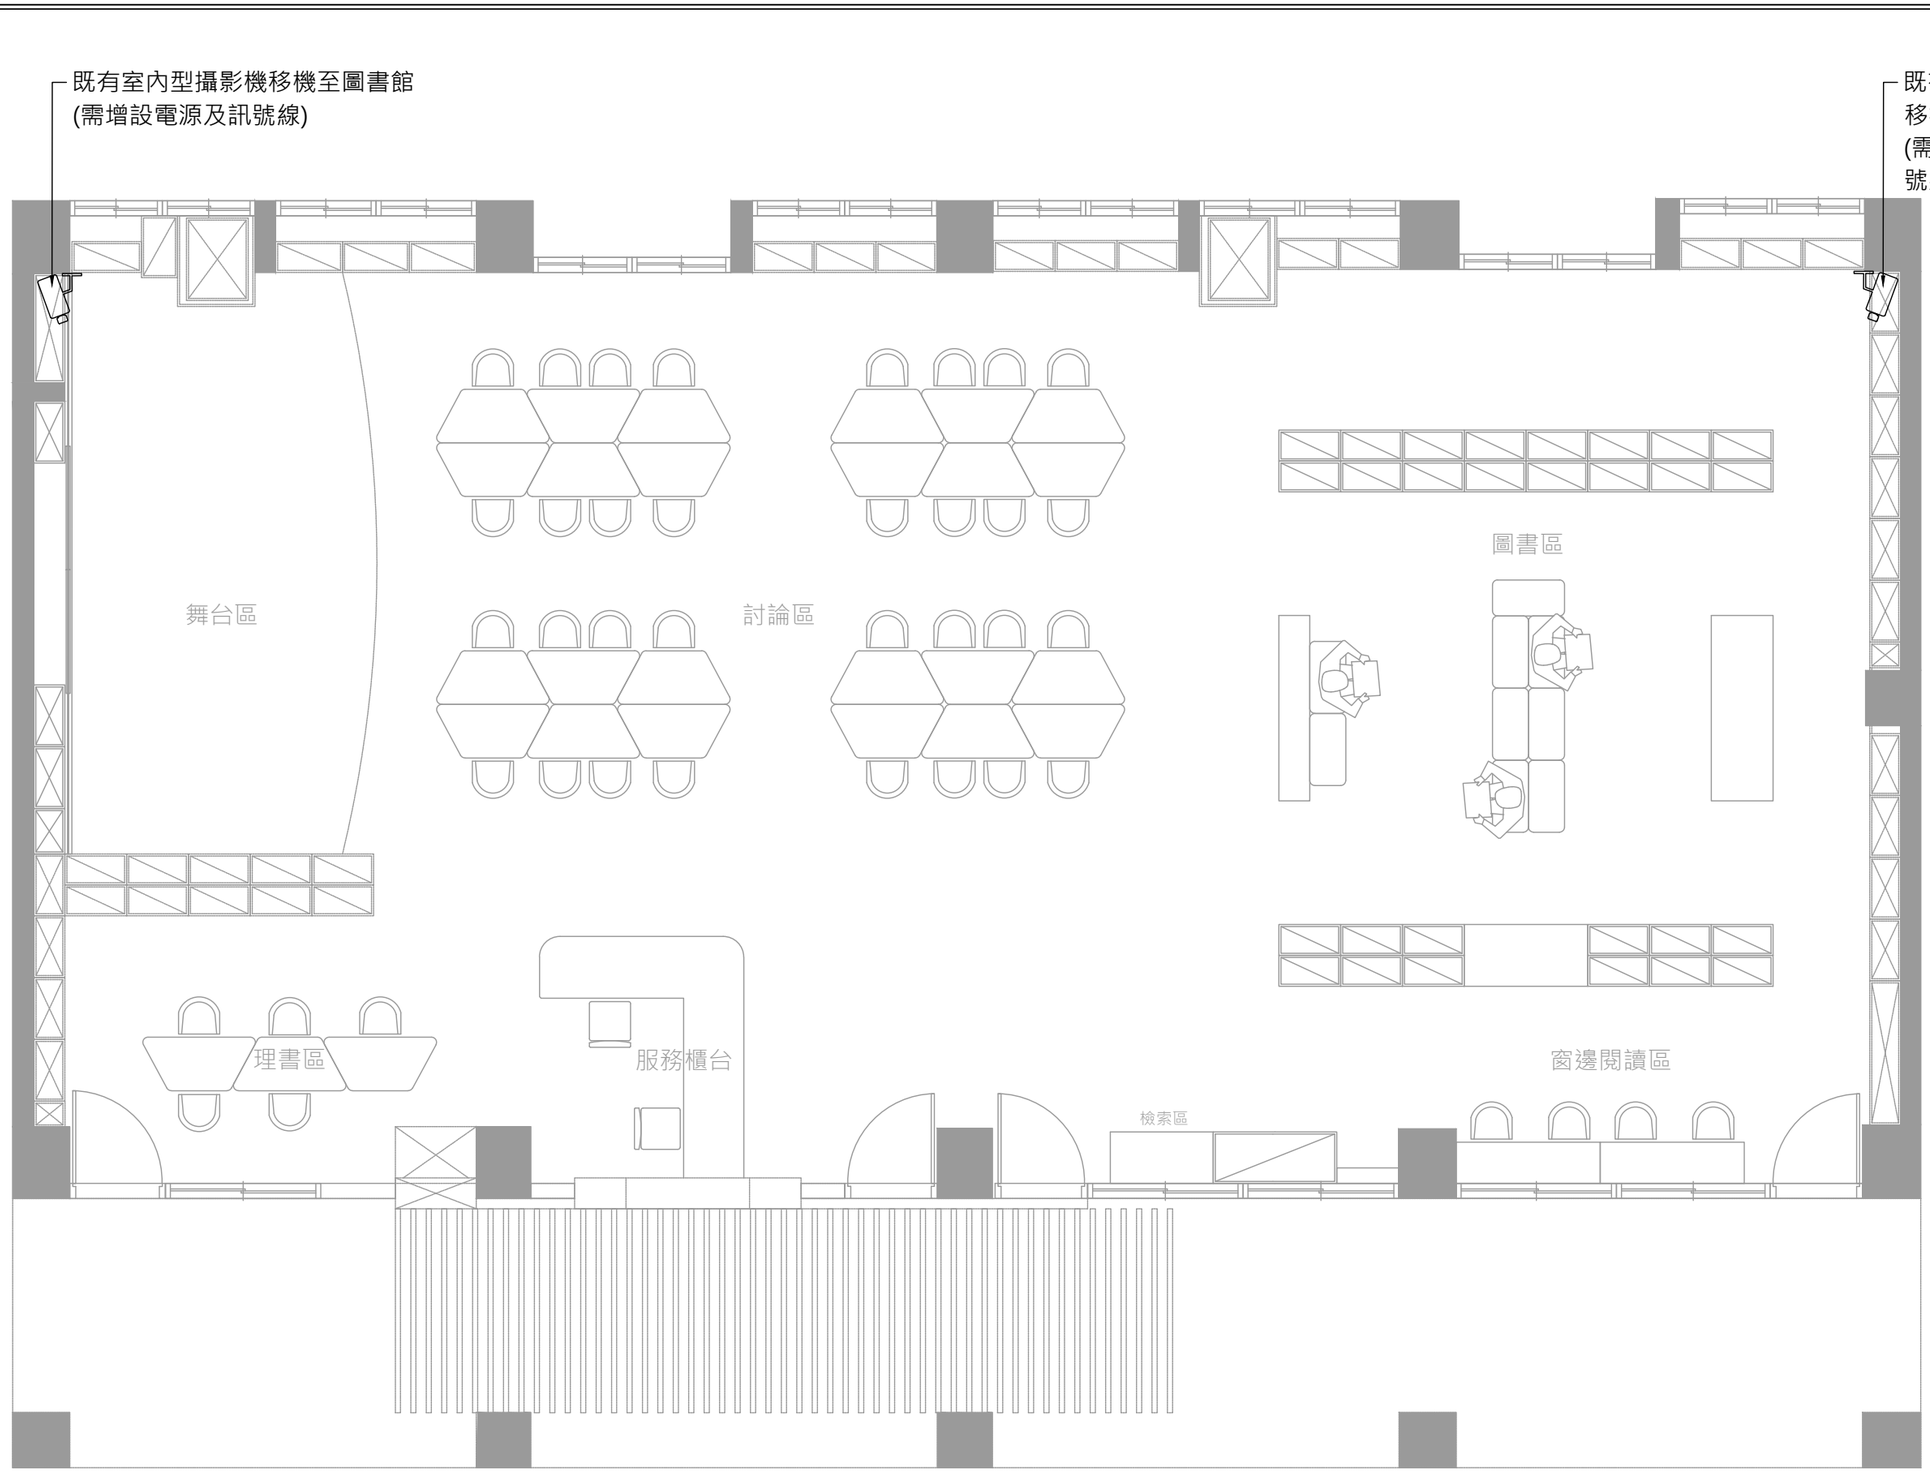

※以上圖說設備主機沿用。
※依實際狀況調整。

工程名稱 PROJECT

永貞國小圖書館整修工程

圖號 DRAWNG NO.	張號 SHEET NO.
	11/32

圖面修正 REVISISONS

NO.	日期 DATE	內容 REMARKS

圖面名稱 DRAWNGTITLE

新設監視器配置圖

張薰和建築師事務所
苗栗市國華路158號2樓
電話:037-263019
傳真:037-263851

圖 說 NOTE

起造人及承造人遵守事項

1.起造人於施工前,務請地政機關鑑定界址,所有尺寸以地政機關鑑界為準,依照實際基地範圍內配合政府所指定建築線施工,不得越界侵佔鄰地,要勿擅自先行動工,否則如有糾紛或受罰,由起造人自行負法律責任.

2.本設計圖經核准後,起造人及承造人必須申報開工,按圖施工,並按進度提請查驗報告,以備完工時申領使用執照.

3.請切實按核准圖樣施工,如原計劃有未盡理想之處,欲予變更時,務須事先辦理變更設計手續,經核准後再行施工,以符法令,切勿擅自變更,否則其後果由起造人承造人負全責.

4.建造房屋必須請合法且無欠稅之營造廠承造.

5.所有基礎,樑柱,樓地板,鋼筋,裝妥後,請起造人知會建築師查驗合格後,才准澆注混凝土.


6.必須注意鄰居房屋之安全,及行人之安全,並不可將建築物材料堆置於道路上妨礙交通.

7.房屋完工後,立即拆除工寮,並將房屋周圍道路水溝清理修復,然後由承造廠商申請核發使用執照,再憑使用執照申請接通水電設備.

8.如有其他圖說發生之疑問,請即提出研討或向縣市政府建管單位書面查詢,切勿擅自解釋法令或施做.

9.承造人不得使用下列材料: (1) 海砂
(2) 輻射鋼筋

比例 SCALE	
設計 DESIGN BY	
繪圖 DRAWN BY	
校對 CHECK BY	
核准 APPROVED BY	
日期 DATE	

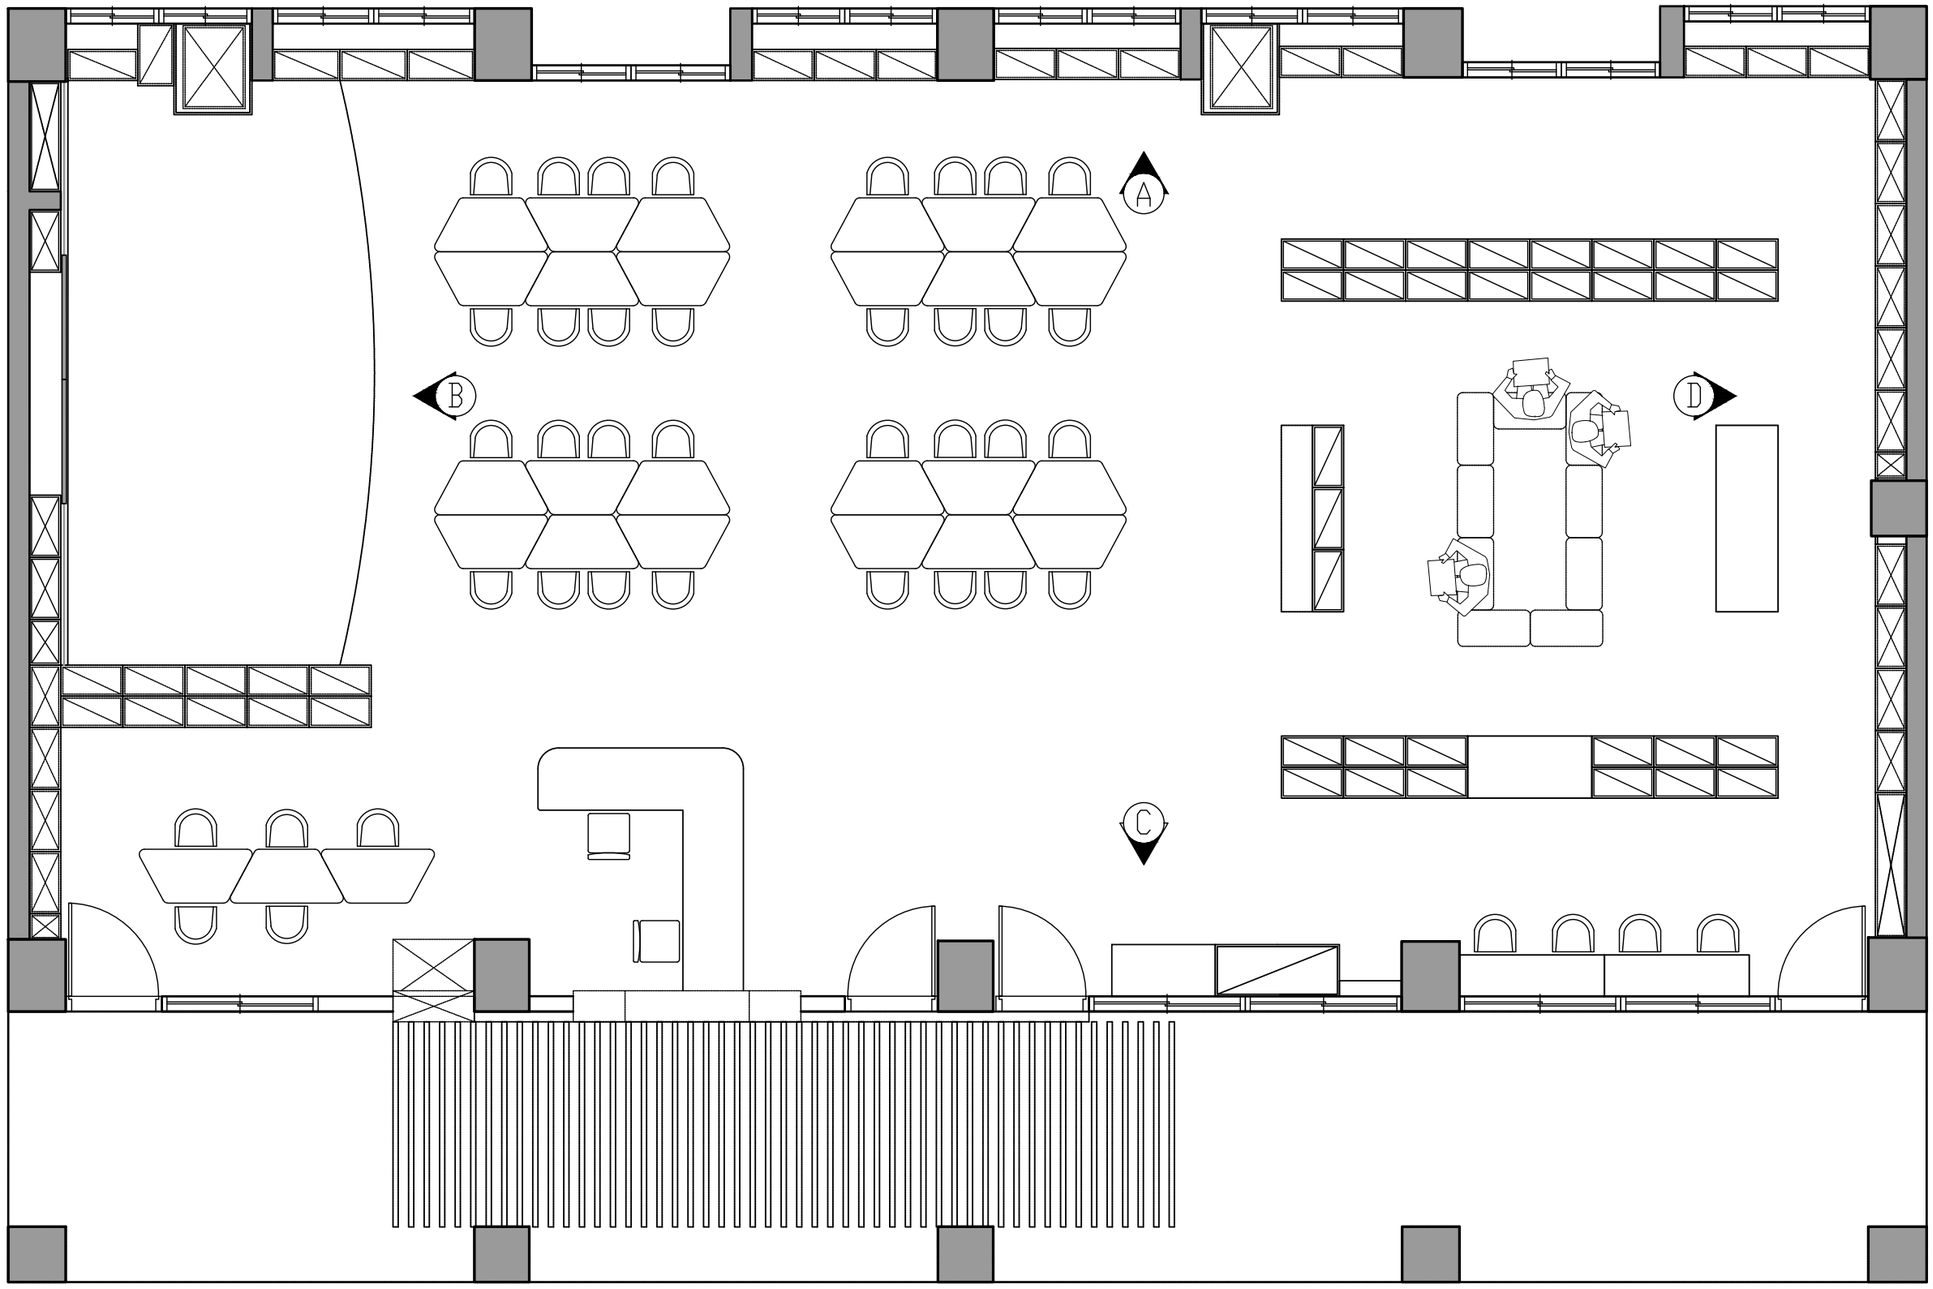

工程名稱 PROJECT

永貞國小圖書館整修工程

圖號 DRAWNG NO.	張號 SHEET NO.
	12/32

圖面修正 REVISISONS

NO.	日期 DATE	內容 REMARKS

圖面名稱 DRAWNGTITLE

立面索引圖

張薰和建築師事務所

苗栗市國華路158號2樓

電話:037-263019

傳真:037-263851

圖說 NOTE

起造人及承造人遵守事項

1.起造人於施工前,務請地政機關鑑定界址,所有尺寸以地政機關鑑界為準,依照實際基地範圍內配合政府所指定建築線施工,不得越界侵佔鄰地,要勿擅自先行動工,否則如有糾紛或受罰,由起造人自行負法律責任.

2.本設計圖經核准後,起造人及承造人必須申報開工,按圖施工並按進度提請查驗報告,以備完工時申領使用執照.

3.請切實按核准圖樣施工,如原計劃有未盡理想之處,欲予變更時,務須事先辦理變更設計手續,經核准後再行施工,以符法令,切勿擅自變更,否則其後果由起造人承造人負全責.

4.建造房屋必須請合法且無欠稅之營造廠承造.

5.所有基礎,樑柱,樓地板,鋼筋,紮妥後,請起造人知會建築師查驗合格後,才准灌注混凝土.


6.必須注意鄰居房屋之安全,及行人之安全,並不可將建築物材料堆置於道路上妨礙交通.


7.房屋完工後,立即拆除工寮,並將房屋周圍臨路水溝清理修復,然後由承造廠商申請核發使用執照,再憑使用執照申請接通水電設備.

8.如有其他臨時發生之疑問,請即提出研討或向縣市政府建管單位書面查詢,切勿擅自解釋法令或臆做.

9.承造人不得使用下列材料:
(1) 海砂
(2) 輻射鋼筋

比例 SCALE	
設計 DESIGN BY	
繪圖 DRAWN BY	
校對 CHECK BY	
核准 APPROVED BY	
日期 DATE	

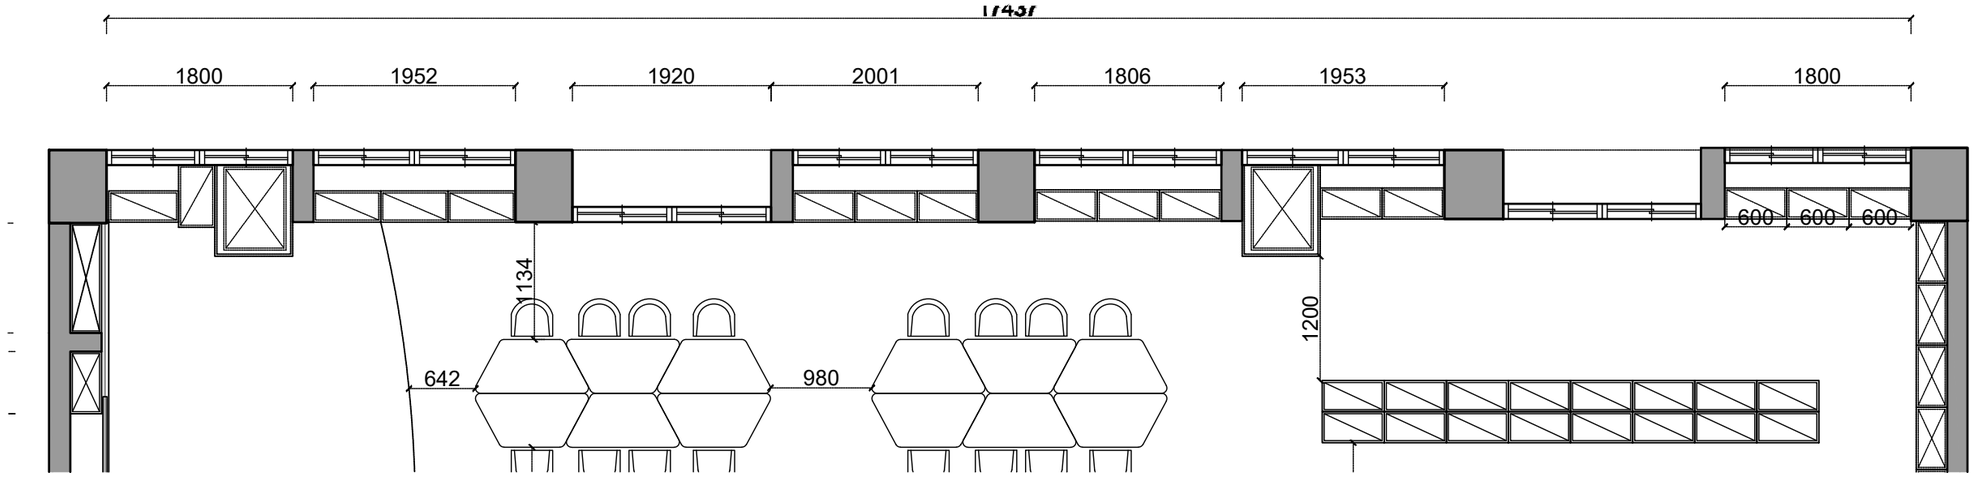

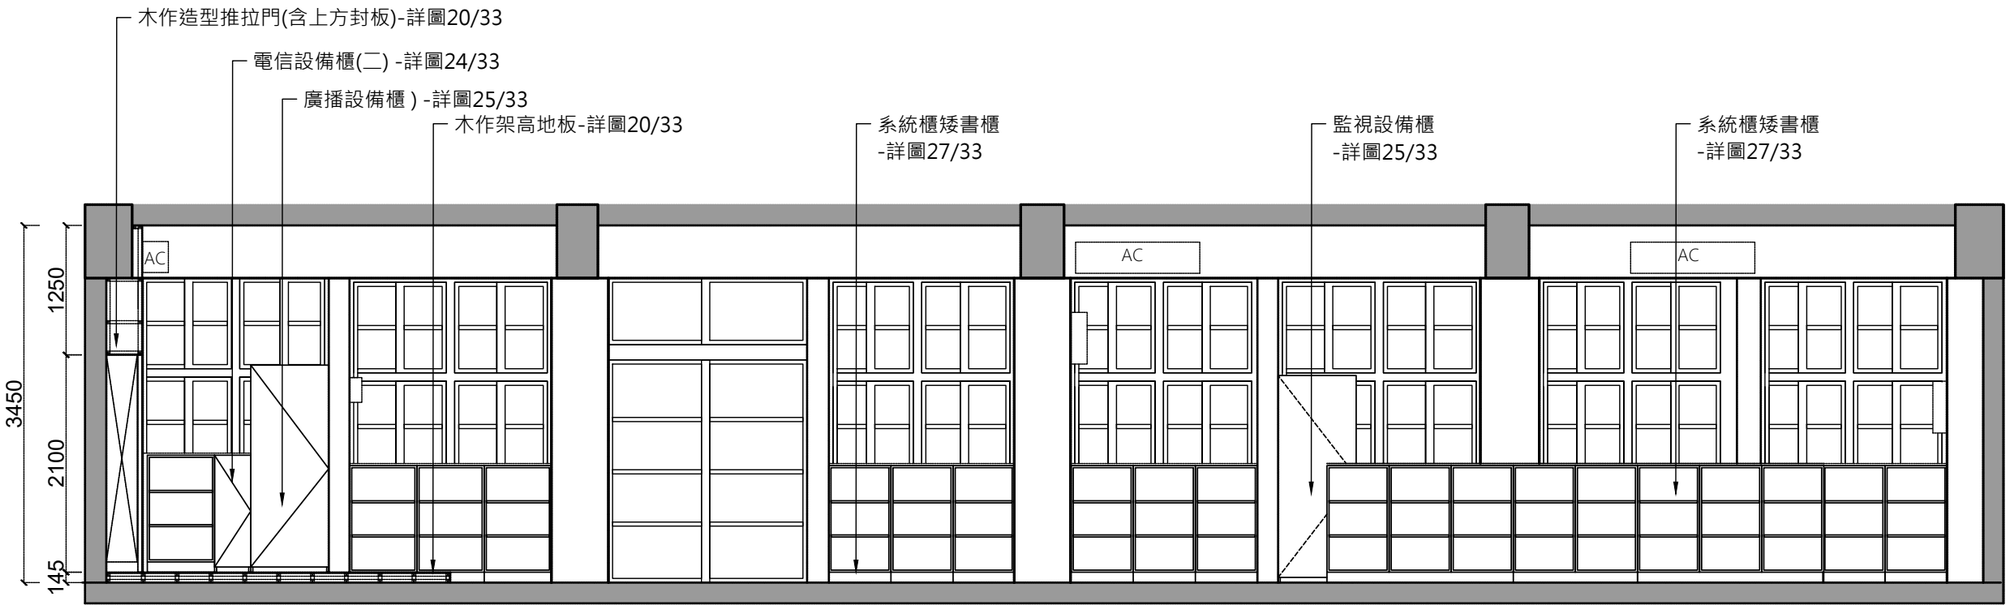

工程名稱 PROJECT

永貞國小圖書館整修工程

圖號 DRAWNG NO.	張號 SHEET NO.
	13/32

圖面修正 REVISISONS

NO.	日期 DATE	內容 REMARKS

圖面名稱 DRAWNGTITLE

A向立面圖

張薰和建築師事務所

苗栗市國華路158號2樓

電話:037-263019

傳真:037-263851

圖 說 NOTE

起造人及承造人遵守事項

1.起造人於施工前,務請地政機關鑑定界址,所有尺寸以地政機關鑑界為準,依照實際基地範圍內配合政府所指定建築線施工,不得超界侵佔鄰地,更勿遷移先行動工,否則如有糾紛或受罰,由起造人自行負法律責任.

2.本設計圖經核准後,起造人及承造人必須申報開工,按圖施工,並按進度提請查驗報告,以備完工時申領使用執照.

3.請切實按核准圖樣施工,如原計劃有未盡理想之處,欲予變更時,務須事先辦理變更設計手續,經核准後再行施工,以符法令,切勿擅自變更,否則其後果由起造人承造人負全責.

4.建造房屋必須請合法且無欠稅之營造廠承造.

5.所有基礎,樑柱,樓地板,鋼筋,紮妥後,請起造人知會建築師查驗合格後,才准灌注混凝土.


6.必須注意鄰居房屋之安全,及行人之安全,並不可將建築物材料堆置於道路上妨礙交通.


7.房屋完工後,立即拆除工寮,並將房屋周圍路水溝清理修復,然後由承造廠商申請核發使用執照,再憑使用執照申請接通水電設備.

8.如有其他臨時發生之疑問,請即提出研討或向縣市政府建管單位書面查詢,切勿擅自解釋法令或臆做.

9.承造人不得使用下列材料: (1) 海砂
(2) 輻射鋼筋

比例 SCALE	
設計 DESIGN BY	
繪圖 DRAWN BY	
校對 CHECK BY	
核准 APPROVED BY	
日期 DATE	

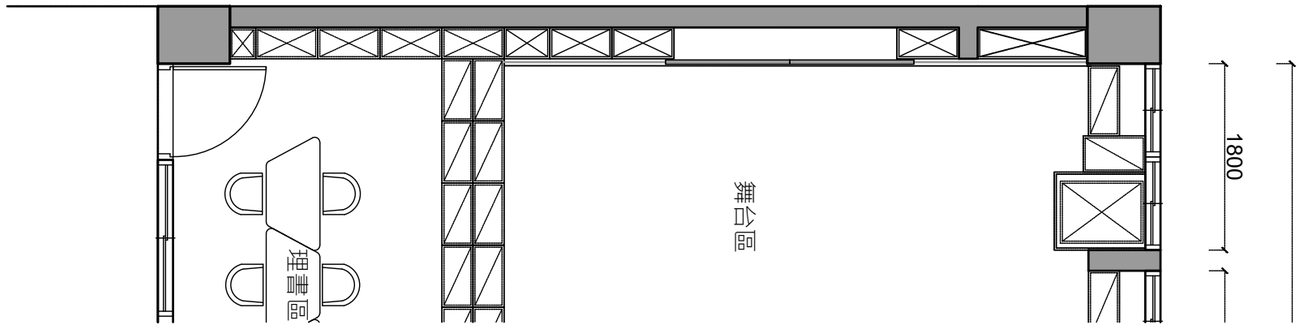

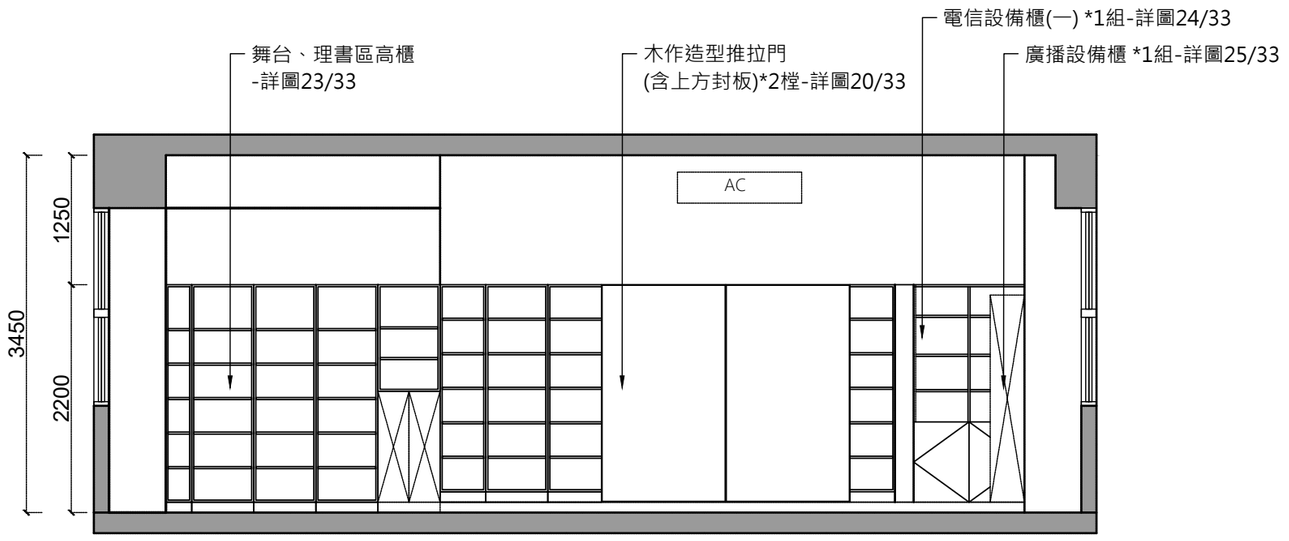

工程名稱 PROJECT

永貞國小圖書館整修工程

圖號 DRAWNG NO.	張號 SHEET NO.
	14/32

圖面修正 REVISISONS

NO.	日期 DATE	內容 REMARKS

圖面名稱 DRAWNGTITLE

B向立面圖

張薰和建築師事務所
苗栗市國華路158號2樓
電話:037-263019
傳真:037-263851

圖 說 NOTE

起造人及承造人遵守事項

1.起造人於施工前,務請地政機關鑑定界址,所有尺寸以地政機關鑑界為準,依照實際基地範圍內配合政府所指定建築線施工,不得越界侵佔鄰地,更勿僅自先行動工,否則所有糾紛或受罰,由起造人自行負法律責任.

2.本設計圖經核准後,起造人及承造人必須申報開工,按圖施工,並按進度提請查驗報告,以備完工時申領使用執照.

3.請切實按核准圖樣施工,如原計劃有未盡理想之處,欲予變更時,務須事先辦理變更設計手續,經核准後再行施工,以符法令,切勿擅自變更,否則其後果由起造人承造人負全責.

4.建造房屋必須請合法且無欠稅之營造廠承造.

5.所有基礎,樑柱,樓地板,鋼筋,紮妥後,請起造人知會建築師簽驗合格後,才准灌注混凝土.


6.必須注意鄰居房屋之安全,及行人之安全,並不可將建築物材料堆置於道路上妨礙交通.


7.房屋完工後,立即拆除工寮,並將房屋周圍道路水溝清理修復,然後由承造廠商申請核發使用執照,再憑使用執照申請接通水電設備.

8.如有其他臨時發生之疑問,請即提出研討或向縣市政府建管單位書面查詢,切勿擅自解釋法令或臆做.

9.承造人不得使用下列材料: (1) 海砂 (2) 輻射鋼筋

比例 SCALE	
設計 DESIGN BY	
繪圖 DRAWN BY	
校對 CHECK BY	
核准 APPROVED BY	
日期 DATE	

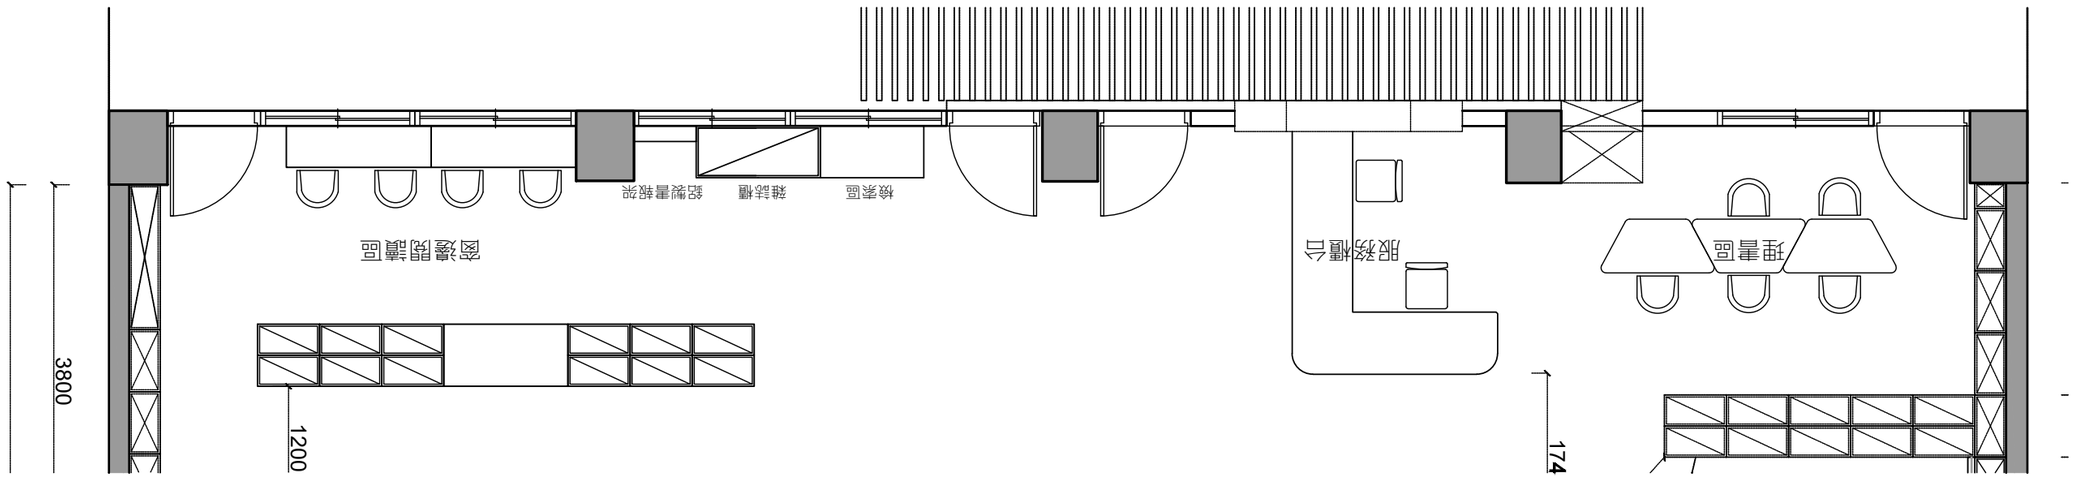

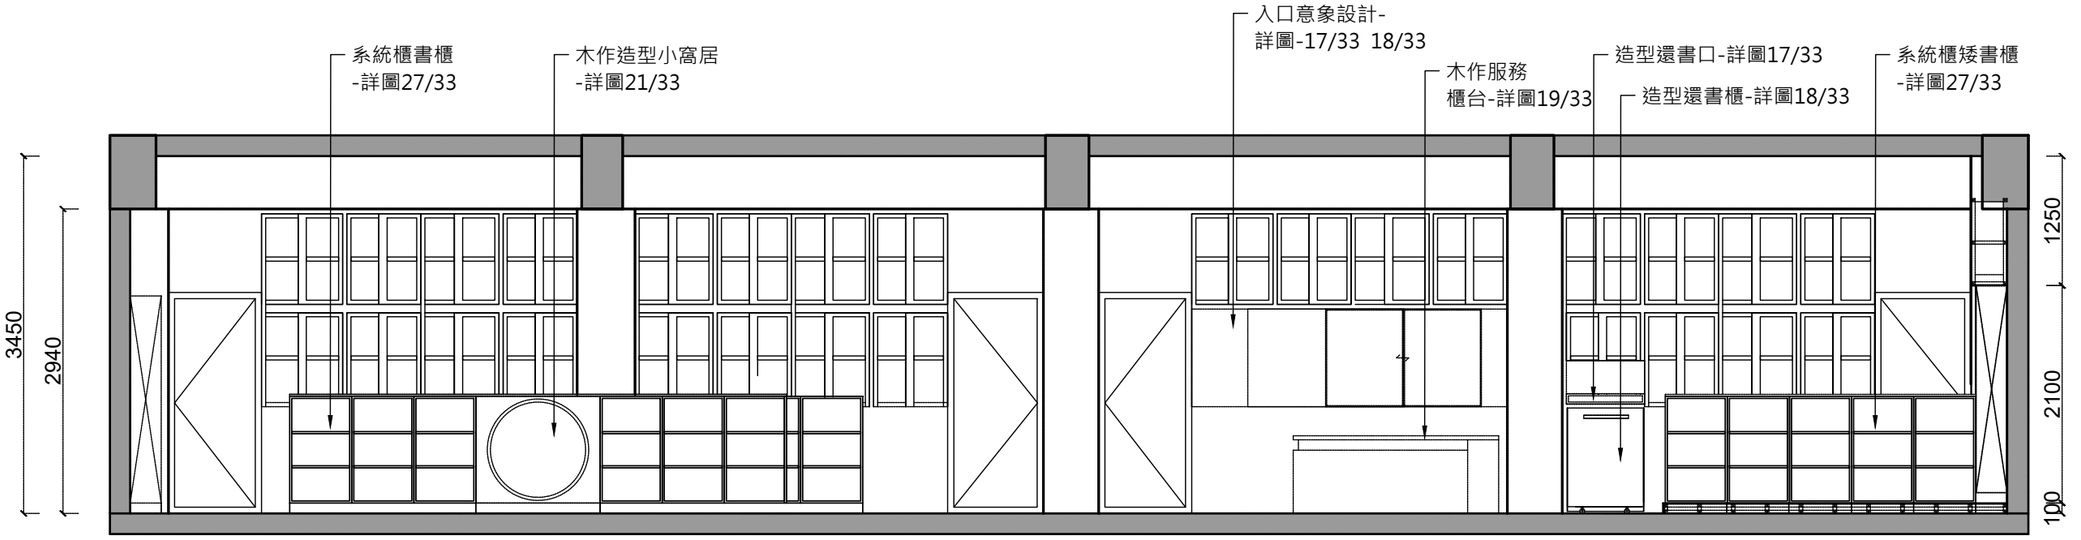

工程名稱 PROJECT

永貞國小圖書館整修工程

圖號 DRAWNG NO.	張號 SHEET NO.
	15/32

圖面修正 REVISISONS

NO.	日期 DATE	內容 REMARKS

圖面名稱 DRAWNGTITLE

C向立面圖

張薰和建築師事務所

苗栗市國華路158號2樓

電話:037-263019

傳真:037-263851

圖 說 NOTE

起造人及承造人遵守事項

1.起造人於施工前,務請地政機關鑑定界址,所有尺寸以地政機關鑑界為準,依照實際基地範圍內配合政府所指定建築線施工,不得越界佔用地,更勿擅自先行動工,否則倘有糾紛或受罰,由起造人自行負法律責任.

2.本設計圖經核准後,起造人及承造人必須申報開工,按圖施工,並按進度提請查驗報告,以備完工時申領使用執照.

3.請切實按核准圖樣施工,如原計劃有未盡理想之處,欲予變更時,務須事先辦理變更設計手續,經核准後再行施工,以符法令,切勿擅自變更,否則其後果由起造人承造人負全責.

4.建造房屋必須請合法且無欠稅之營造廠承造.

5.所有基礎,樑柱,樓地板,鋼筋,紮妥後,請起造人知會建築師簽驗合格後,才准灌注混凝土.


6.必須注意鄰居房屋之安全,及行人之安全,並不可將建築物材料堆置於道路上妨礙交通.


7.房屋完工後,立即拆除工寮,並將房屋周圍道路水溝清理修復,然後由承造廠商申請核發使用執照,再憑使用執照申請接通水電設備.

8.如有其他臨時發生之疑問,請即提出研討或向縣市政府建管單位書面查詢,切勿擅自解釋法令或臆度.

9.承造人不得使用下列材料: (1) 海砂 (2) 輻射鋼筋

比例 SCALE	
設計 DESIGN BY	
繪圖 DRAWN BY	
校對 CHECK BY	
核准 APPROVED BY	
日期 DATE	

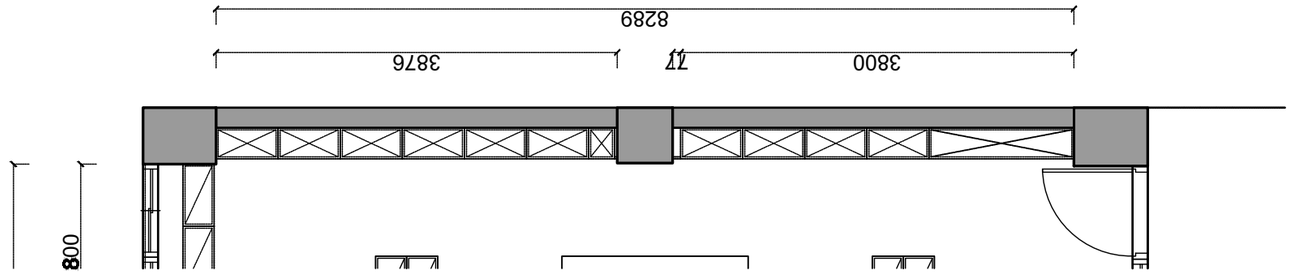

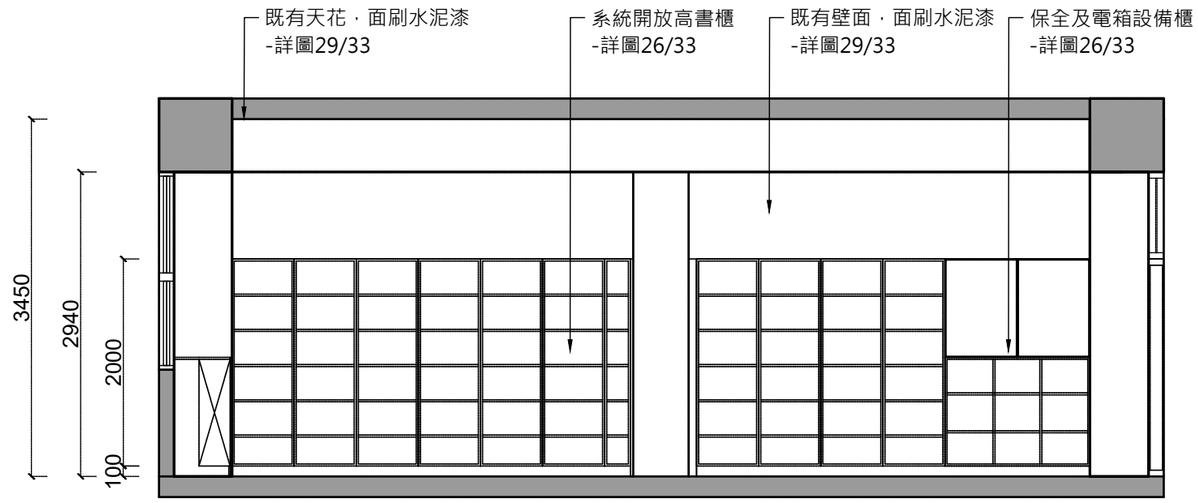

工程名稱 PROJECT

永貞國小圖書館整修工程

圖號 DRAWNG NO.	張號 SHEET NO.
	16/32

圖面修正 REVISISONS

NO.	日期 DATE	內容 REMARKS

圖面名稱 DRAWNGTITLE

D向立面圖

張薰和建築師事務所
苗栗市國華路158號2樓
電話:037-263019
傳真:037-263851

圖 說 NOTE

起造人及承造人遵守事項

1.起造人於施工前,務請地政機關鑑定界址,所有尺寸以地政機關鑑界為準,依照實際基地範圍內配合政府所指定建築線施工,不得越界侵佔鄰地,更勿遷自先行動工,否則如有糾紛或受罰,由起造人自行負法律責任.

2.本設計圖經核准後,起造人及承造人必須申報開工,按圖施工,並按進度提請查驗報告,以備完工時申領使用執照.

3.請切實按核准圖樣施工,如原計劃有未盡理想之處,欲予變更時,務須事先辦理變更設計手續,經核准後再行施工,以符法令,切勿擅自變更,否則其後果由起造人承造人負全責.

4.建造房屋必須請合法且無欠稅之營造廠承造.

5.所有基礎,樑柱,樓地板,鋼筋,紮妥後,請起造人知會建築師簽驗合格後,才准灌注混凝土.

6.必須注意鄰居房屋之安全,及行人之安全,並不可將建築物材料堆置於道路上妨礙交通.


7.房屋完工後,立即拆除工寮,並將房屋周圍路水溝清理修復,然後由承造廠商申請核發使用執照,再憑使用執照申請接通水電設備.


8.如有其他圖師發生之疑問,請即提出研討或向縣市政府建管單位書面查詢,切勿擅自解釋法令或施做.

9.承造人不得使用下列材料: (1) 海砂
(2) 輻射鋼筋

比例 SCALE	
設計 DESIGN BY	
繪圖 DRAWN BY	
校對 CHECK BY	
核准 APPROVED BY	
日期 DATE	

入口意象設計

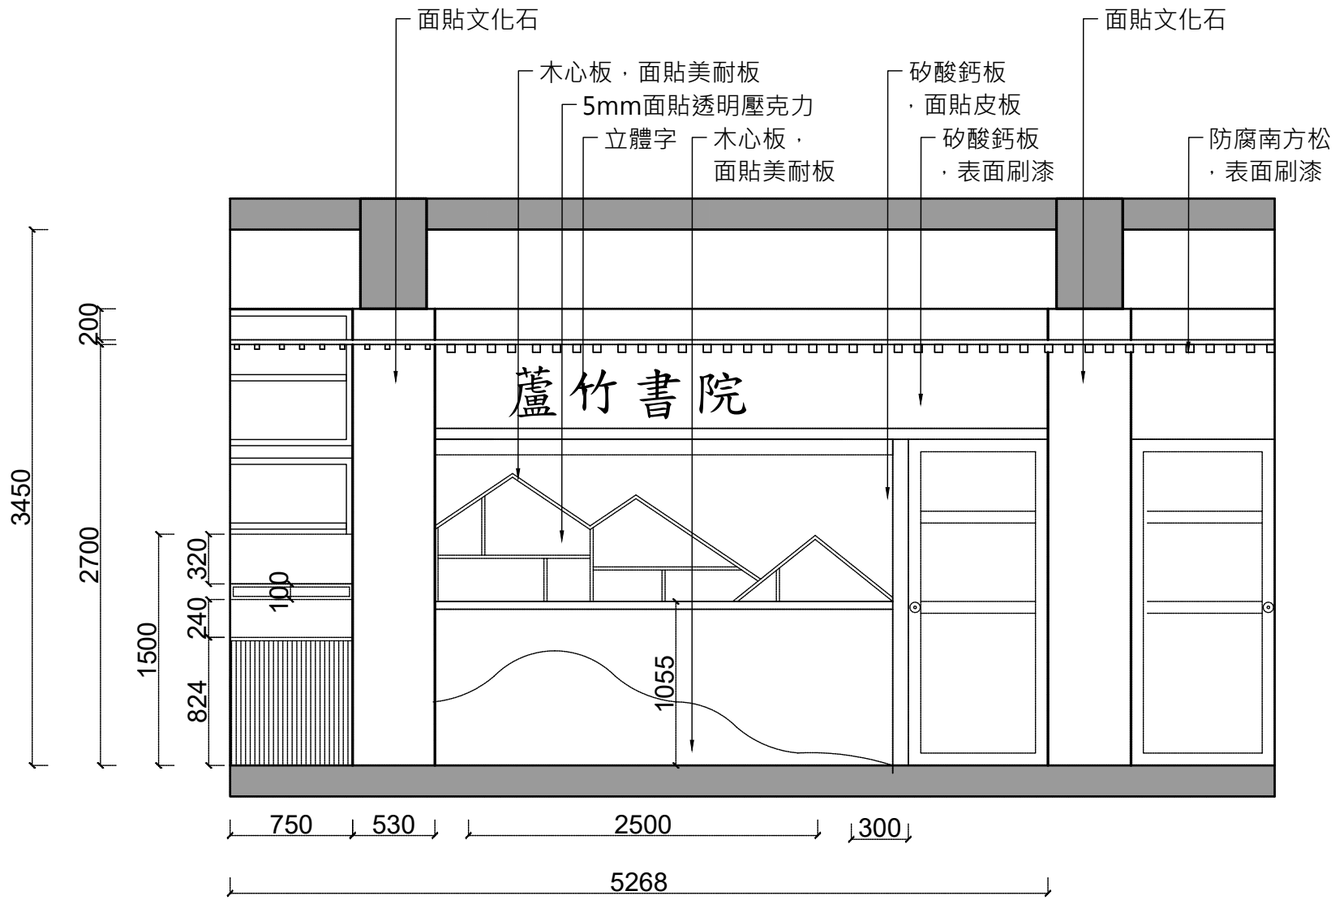

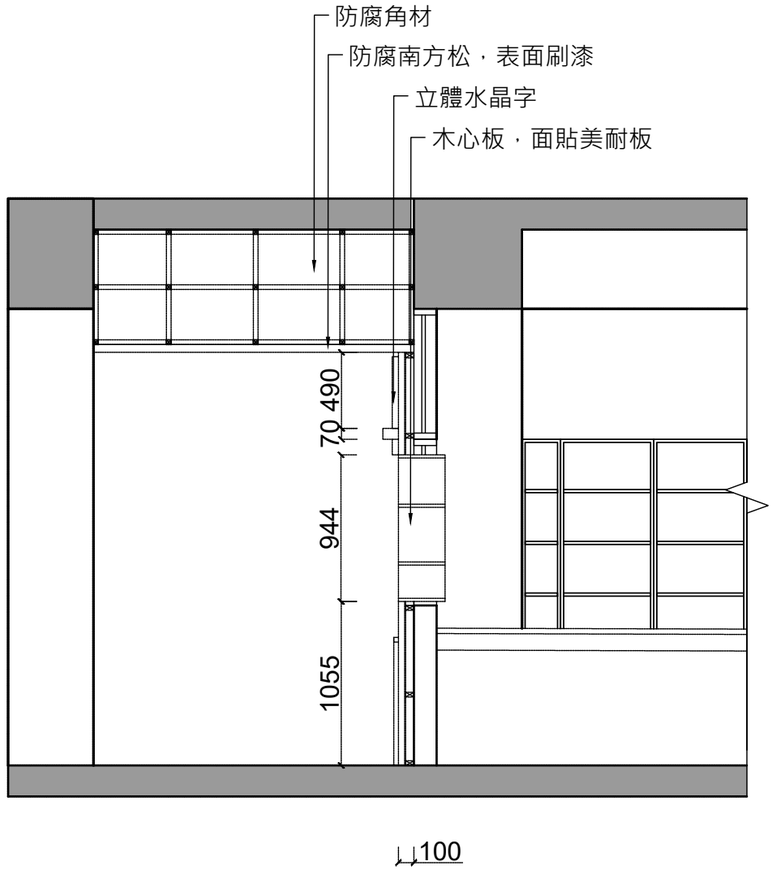

※以上圖說設備顏色另選，需與校方或設計單位確認後方可施作。
※依實際狀況調整。

工程名稱 PROJECT

永貞國小圖書館整修工程

圖號 DRAWNG NO.	張號 SHEET NO.
	17/32

圖面修正 REVISISONS

NO.	日期 DATE	內容 REMARKS

圖面名稱 DRAWNGTITLE

入口意象設計圖

張薰和建築師事務所
苗栗市國華路158號2樓
電話:037-263019
傳真:037-263851


圖 說 NOTE


起造人及承造人遵守事項


1.起造人於施工前,務請地政機關鑑定界址,所有尺寸以地政機關鑑界為準,依照實際基地範圍內配合政府所指定建築線施工,不得越界侵佔鄰地,要勿擅自先行動工,否則如有糾紛或受罰,由起造人自行負法律責任。
2.本設計圖經核准後,起造人及承造人必須申報開工,按圖施工,並按進度提請查驗報告,以備完工時申領使用執照。
3.請切實按核准圖樣施工,如原計劃有未盡理想之處,敬予變更時,務須事先辦理變更設計手續,經核准後再行施工,以符法令,切勿擅自變更,否則其後果由起造人承造人負全責。
4.建造房屋必須請合法且無欠稅之營造廠承造。
5.所有基礎,樑柱,樓地板,鋼筋,裝妥後,請起造人知會建築師查驗合格後,才准灌注混凝土。
6.必須注意鄰居房屋之安全,及行人之安全,並不可將建築物材料堆置於道路上妨礙交通。
7.房屋完工後,立即拆除工寮,並將房屋周圍雜草水溝清理妥當,然後由承造廠商申請核發使用執照,再憑使用執照申請接通水電設備。
8.如有其他臨時發生之疑問,請即提出研討或向縣市政府建管單位書面查詢,切勿擅自解釋法令或施做。
9.承造人不得使用下列材料:
(1) 海砂
(2) 輻射鋼筋

比例 SCALE	
設計 DESIGN BY	
繪圖 DRAWN BY	
校對 CHECK BY	
核准 APPROVED BY	
日期 DATE	

入口意象設計(二)

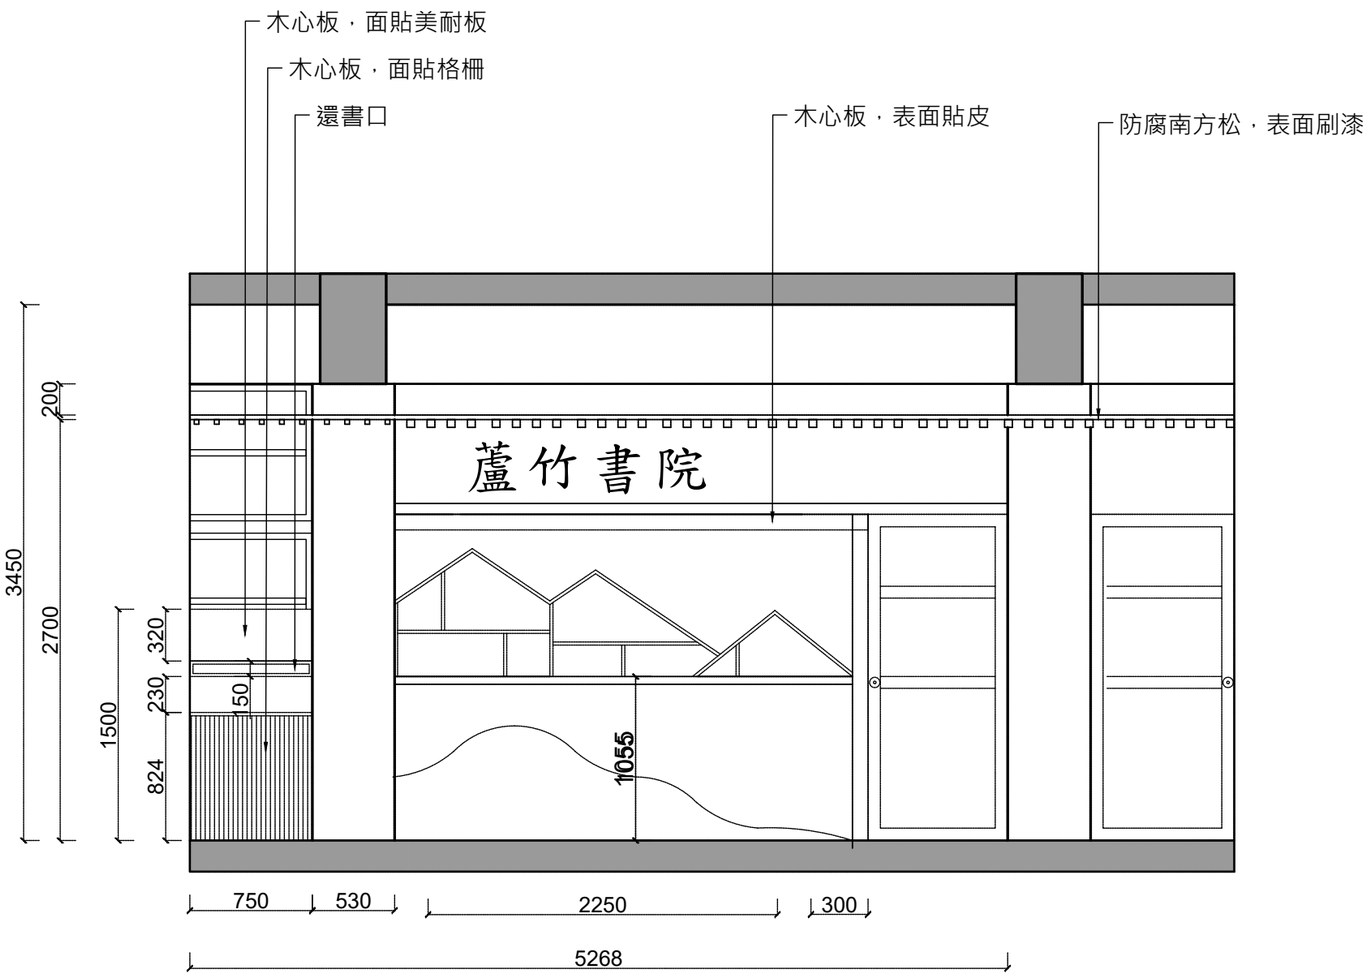

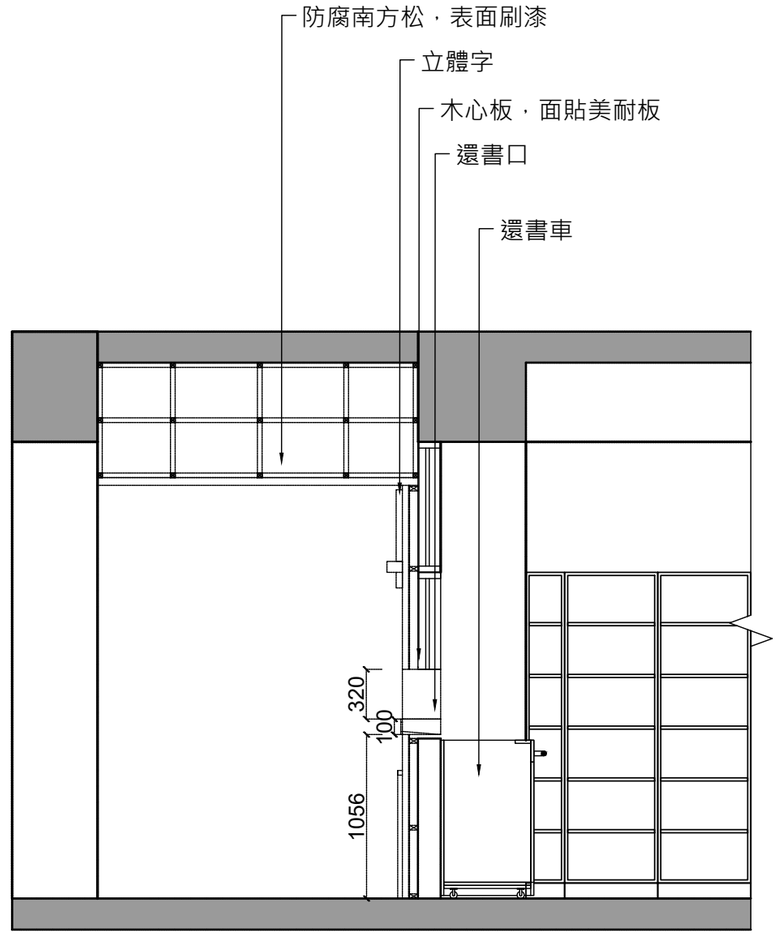

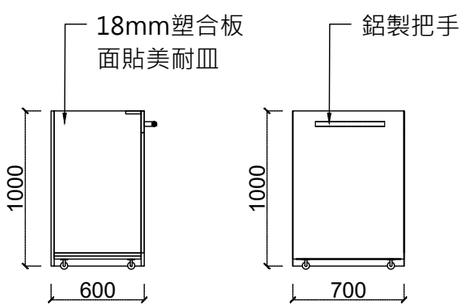

還書推車

※以上圖說設備顏色另選，需與校方或設計單位確認後方可施作
※依實際狀況調整。

工程名稱 PROJECT

永貞國小圖書館整修工程

圖號 DRAWNG NO.

張號 SHEET NO.

18/32

圖面修正 REVISISONS

NO.	日期 DATE	內容 REMARKS

圖面名稱 DRAWNGTITLE

入口意象設計圖(二))

張薰和建築師事務所
苗栗市國華路158號2樓
電話:037-263019
傳真:037-263851

圖 說 NOTE

起造人及承造人遵守事項

1.起造人於施工前,務請地政機關鑑定界址,所有尺寸以地政機關鑑界為準,依照實際基地範圍內配合政府所指定建築線施工,不得越界侵佔鄰地,界方僅供先行動工,否則如有糾紛或受罰,由起造人自行負法律責任.

2.本設計圖經核准後,起造人及承造人必須申報開工,按圖施工,並按進度提請查驗報告,以備完工時申領使用執照.

3.請切實按核准圖樣施工,如原計劃有未盡理想之處,欲予變更時,務須事先辦理變更設計手續,經核准後再行施工,以符法令,切勿擅自變更,否則其後果由起造人承造人負全責.

4.建造房屋必須請合法且無欠稅之營造廠承造.

5.所有基礎,樑柱,樓地板,鋼筋,紮妥後,請起造人知會建築師查驗合格後,才准灌注混凝土.

6.必須注意鄰居房屋之安全,及行人之安全,並不可將建築物材料堆置於道路上妨礙交通.


7.房屋完工後,立即拆除工寮,並將房屋用圍籬路水溝清理修復,然後由承造廠商申請核發使用執照,再憑使用執照申請接通水電設備.


8.如有其他圖詞發生之疑問,請即提出研討或向轄市政府建管單位書面查詢,切勿擅自解釋法令或施做.


9.承造人不得使用下列材料: (1) 海砂
(2) 輻射鋼筋


比例 SCALE	
設計 DESIGN BY	
繪圖 DRAWN BY	
校對 CHECK BY	
核准 APPROVED BY	
日期 DATE	

服務櫃台設計圖

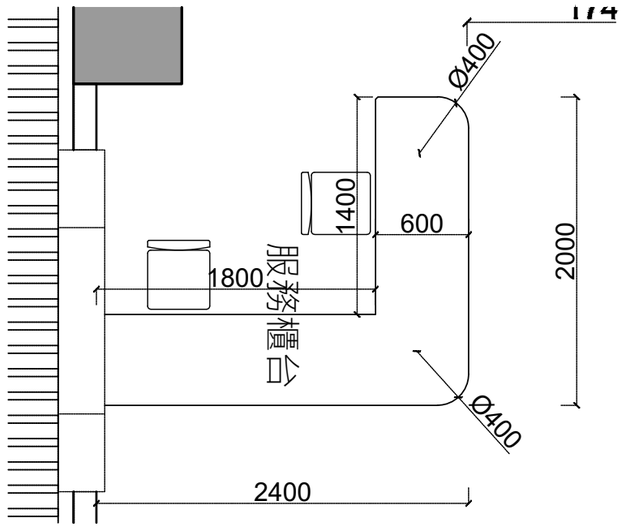

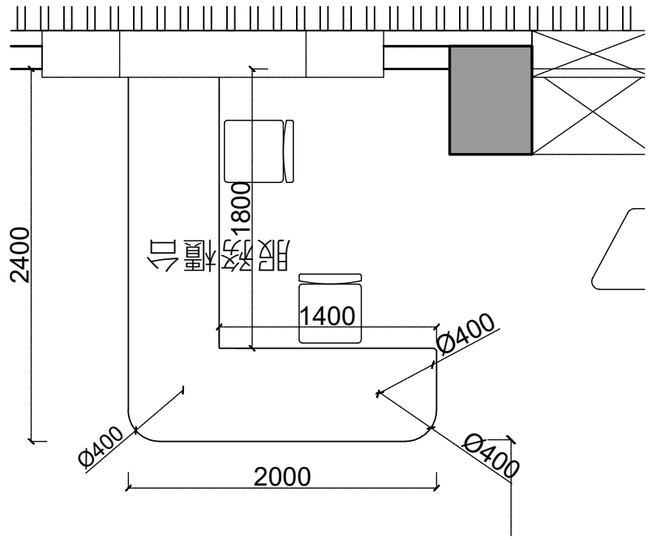

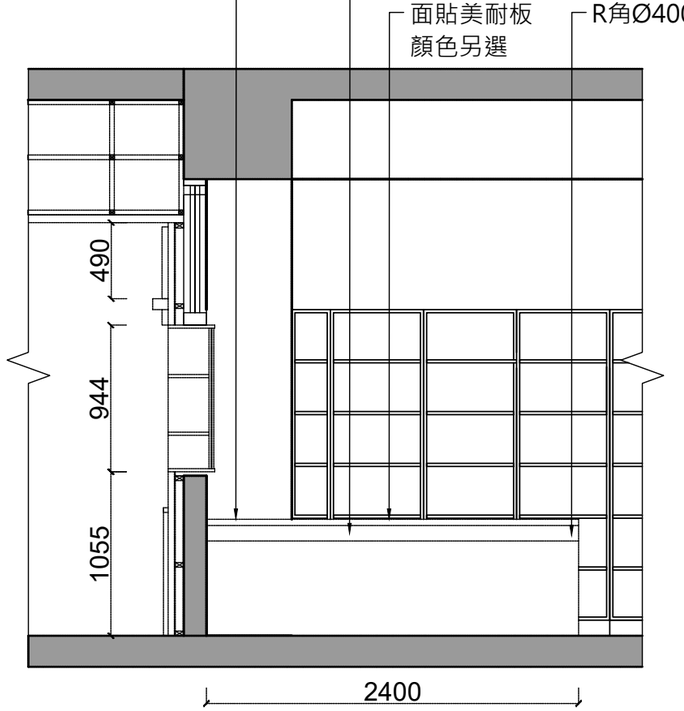

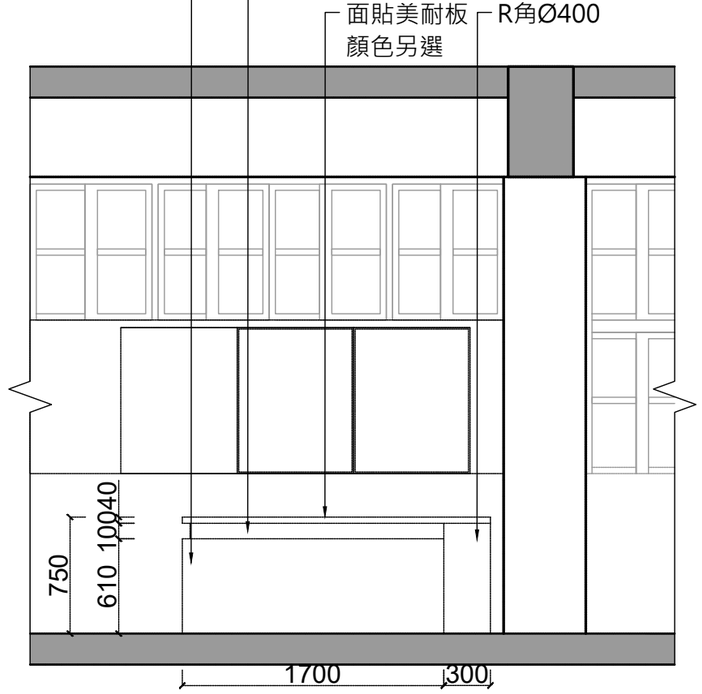

※以上圖說設備顏色另選，需與校方或設計單位確認後方可施作。
※依實際狀況調整。

工程名稱 PROJECT

永貞國小圖書館整修工程

圖號 DRAWNG NO.	張號 SHEET NO.
	19/32

圖面修正 REVISISONS

NO.	日期 DATE	內容 REMARKS

圖面名稱 DRAWNGTITLE

服務櫃台設計圖

張薰和建築師事務所
苗栗市國華路158號2樓
電話:037-263019
傳真:037-263851

圖 說 NOTE

起造人及承造人遵守事項

1.起造人於施工前,務請地政機關鑑定界址,所有尺寸以地政機關鑑界為準,依照實際基地範圍內配合政府所指定建築線施工,不得越界侵佔鄰地,更勿擅自先行動工,否則所有糾紛或受罰,由起造人自行負法律責任.

2.本設計圖經核准後,起造人及承造人必須申報開工,按圖施工,並按進度提請查驗報告,以備完工時申領使用執照.

3.請切實按核准圖樣施工,如原計劃有未盡理想之處,欲予變更時,務須事先辦理變更設計手續,經核准後再行施工,以符法令,切勿擅自變更,否則其後果由起造人承造人負全責.

4.建造房屋必須請合法且無欠稅之營造廠承造.

5.所有基礎,樑柱,樓地板,鋼筋,紮妥後,請起造人知會建築師查驗合格後,才准灌注混凝土.

6.必須注意鄰居房屋之安全,及行人之安全,並不可將建築物材料堆置於道路上妨礙交通.


7.房屋完工後,立即拆除工寮,並將房屋周圍排水溝清理修復,然後由承造廠商申請核發使用執照,再憑使用執照申請接通水電設備.


8.如有其他臨時發生之疑問,請即提出研討或向縣市政府建管單位書面查詢,切勿擅自解釋法令或施做.


9.承造人不得使用下列材料: (1) 海砂 (2) 輻射鋼筋

比例 SCALE	
設計 DESIGN BY	
繪圖 DRAWN BY	
校對 CHECK BY	
核准 APPROVED BY	
日期 DATE	

木作造型推拉(含上方封板)

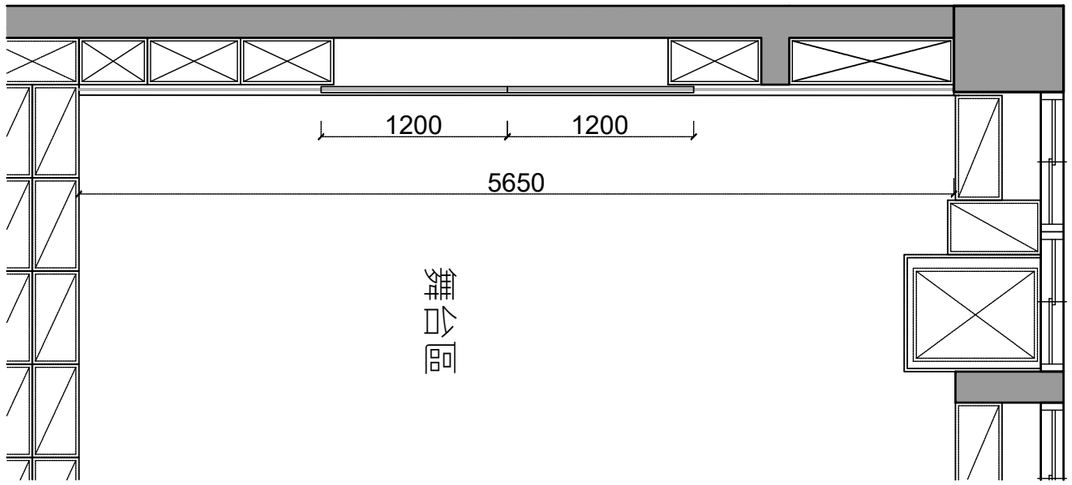

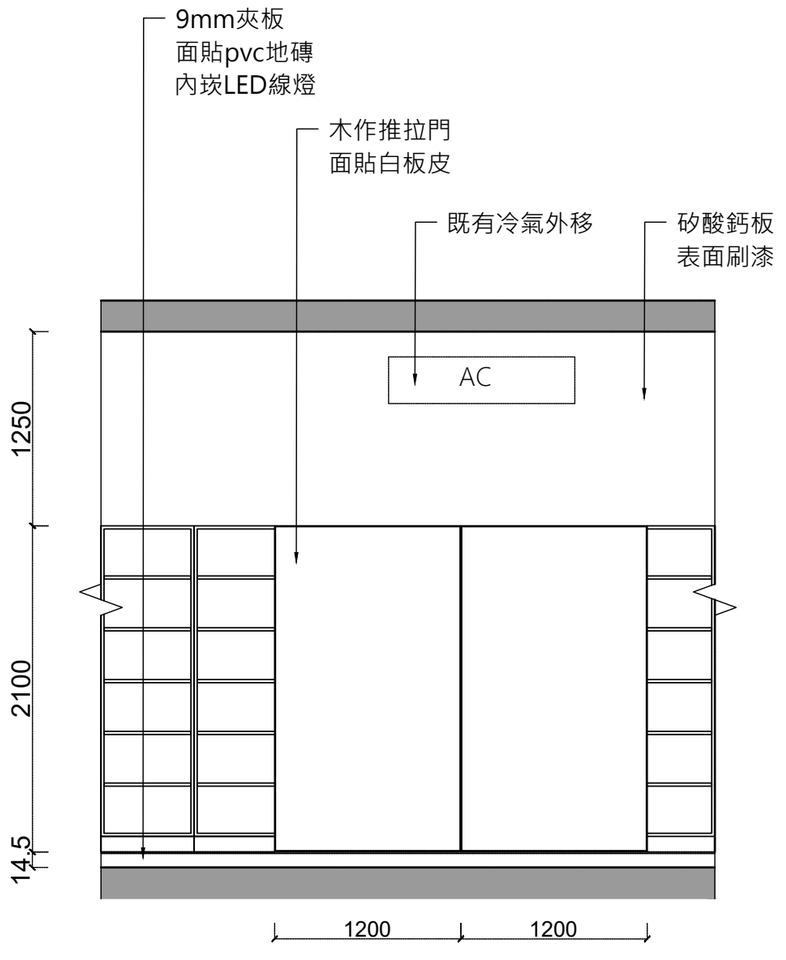

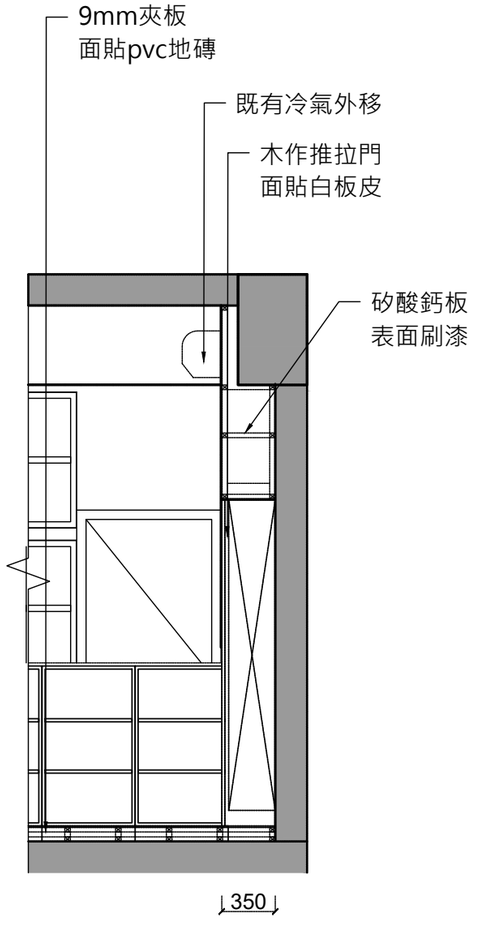

※以上圖說設備顏色另選，需與校方或設計單位確認後方可施作。
※依實際狀況調整。

工程名稱 PROJECT

永貞國小圖書館整修工程

圖號 DRAWNG NO.	張號 SHEET NO.
	20/32

圖面修正 REVISISONS

NO.	日期 DATE	內容 REMARKS

圖面名稱 DRAWNGTITLE

木作造型推拉門-詳圖

張薰和建築師事務所
苗栗市國華路158號2樓
電話:037-263019
傳真:037-263851

圖 說 NOTE

起造人及承造人應守事項

1.起造人於施工前,應請地政機關鑑定界址,所有尺寸以地政機關鑑界為準,依照實際基地範圍內配合政府所指定建築線施工,不得越界侵佔鄰地,要勿擅自先行動工,否則如有糾紛或受罰,由起造人自行負法律責任.

2.本設計圖經核准後,起造人及承造人必須申報開工,按圖施工,並按進度提請查驗報告,以備完工時申領使用執照.

3.請切實按核准圖樣施工,如原計劃有未盡理想之處,欲予變更時,務須事先辦理變更設計手續,經核准後再行施工,以符法令,切勿擅自變更,否則其後果由起造人承造人負全責.

4.建造房屋必須請合法且無欠稅之營造廠承造.

5.所有基礎,樑柱,樓地板,鋼筋,灰妥後,請起造人知會建築師簽驗合格後,才准灌注混凝土.

6.必須注意鄰居房屋之安全,及行人之安全,並不可將建築物材料堆置於道路上妨礙交通.


7.房屋完工後,立即拆除工寮,並將房屋周圍道路水溝清理修復,然後由承造廠商申請核發使用執照,再憑使用執照申請接通水電設備.


8.如有其他疑時發生之疑問,請即提出研討或向縣市政府建管單位書面查詢,切勿擅自解釋法令或施做.

9.承造人不得使用下列材料: (1) 海砂
(2) 輻射鋼筋


比例 SCALE	
設計 DESIGN BY	
繪圖 DRAWN BY	
校對 CHECK BY	
核准 APPROVED BY	
日期 DATE	


大窩居/小窩居設計圖

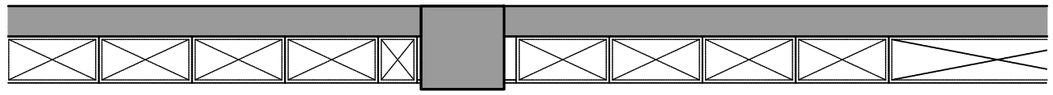

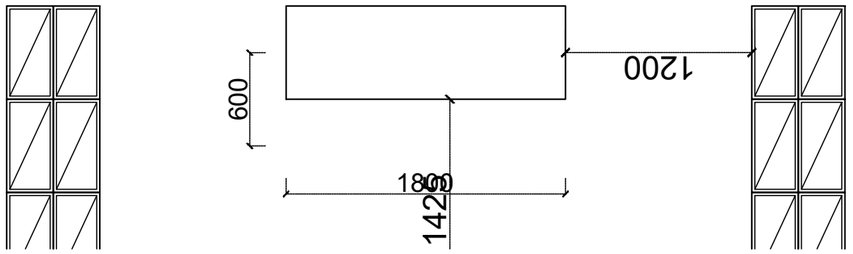


窗邊閱讀區

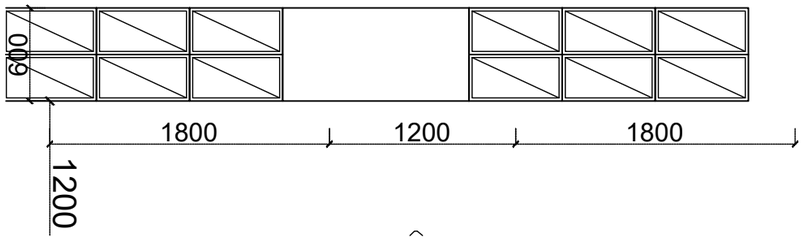

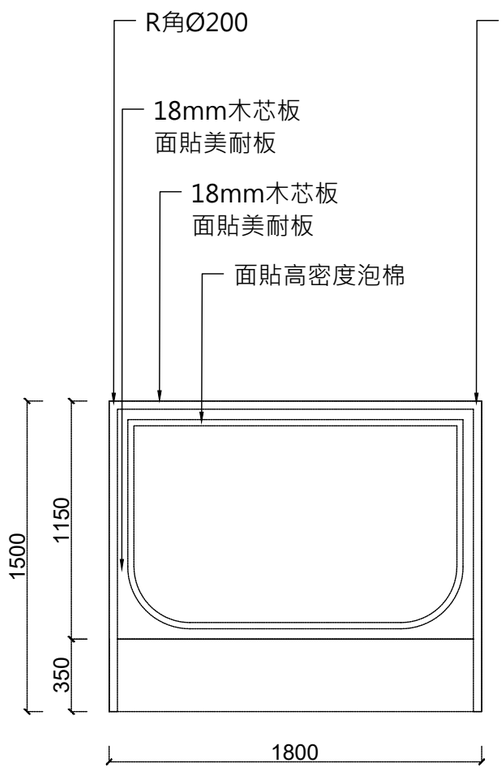

大窩居

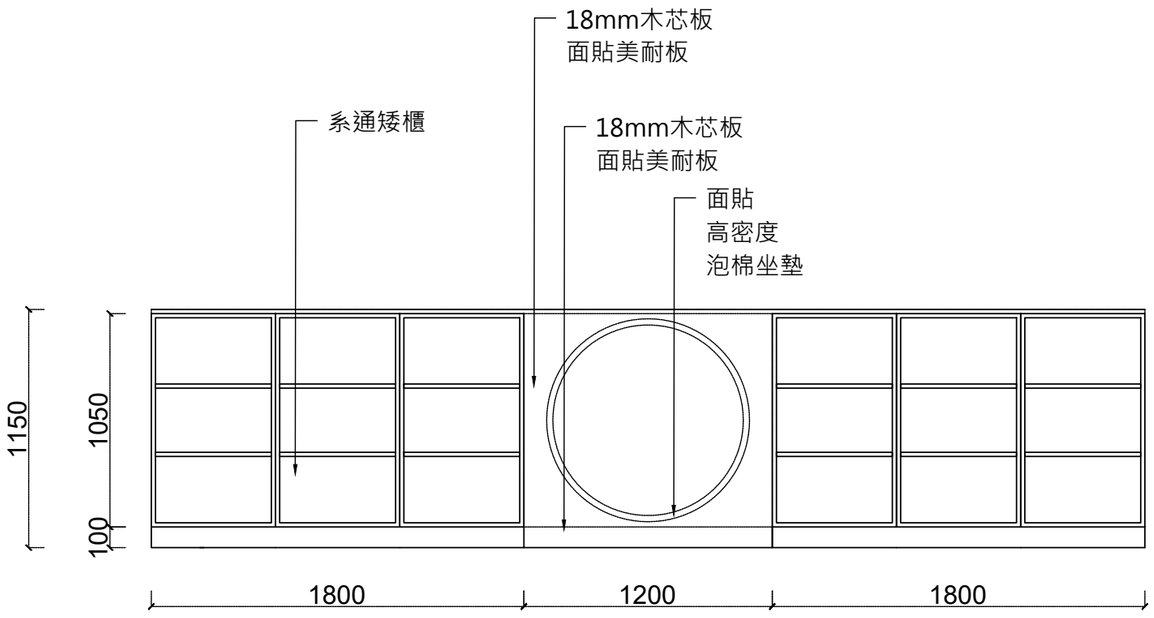

小窩居

※以上圖說設備顏色另選，需與校方或設計單位確認後方可施作。
※依實際狀況調整。

工程名稱 PROJECT

永貞國小圖書館整修工程

圖號 DRAWNG NO.	張號 SHEET NO.
	21/32

圖面修正 REVISISONS

NO.	日期 DATE	內容 REMARKS

圖面名稱 DRAWNGTITLE

大窩居/小窩居設計圖

張薰和建築師事務所
苗栗市國華路158號2樓
電話:037-263019
傳真:037-263851

圖 說 NOTE

起造人及承造人遵守事項

1.起造人於施工前,務請地政機關鑑定界址,所有尺寸以地政機關鑑界為準,依照實際基地範圍內配合政府所指定建築線施工,不得越界侵佔鄰地,更勿擅自先行動工,否則所有糾紛或受罰,由起造人自行負法律責任.

2.本設計圖經核准後,起造人及承造人必須申報開工,按圖施工,並按進度提請查驗報告,以備完工時申領使用執照.

3.請切實按核准圖樣施工,如原計劃有未盡理想之處,欲予變更時,務須事先辦理變更設計手續,經核准後再行施工,以符法令,切勿擅自變更,否則其後果由起造人承造人負責.

4.建造房屋必須請合法且無欠稅之營造廠承造.

5.所有基礎,樑柱,樓地板,鋼筋,紮妥後,請起造人知會建築師查驗合格後,才准灌注混凝土.

6.必須注意鄰居房屋之安全,及行人之安全,並不可將建築物材料堆置於道路上妨礙交通.


7.房屋完工後,立即拆除工寮,並將房屋周圍道路水溝清理修復,然後由承造廠商申請核發使用執照,再憑使用執照申請接通水電設備.

8.如有其他臨時發生之疑問,請即提出研討或向縣市政府建管單位書面查詢,切勿擅自解釋法令或施做.


9.承造人不得使用下列材料: (1) 海砂 (2) 輻射鋼筋


比例 SCALE	
設計 DESIGN BY	
繪圖 DRAWN BY	
校對 CHECK BY	
核准 APPROVED BY	
日期 DATE	

造型新書/期刊/雜誌櫃

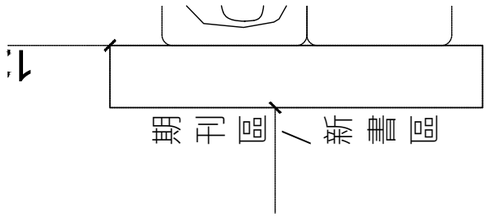



新書/期刊展示櫃

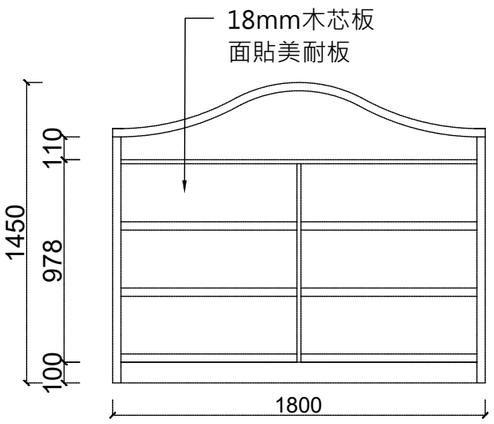

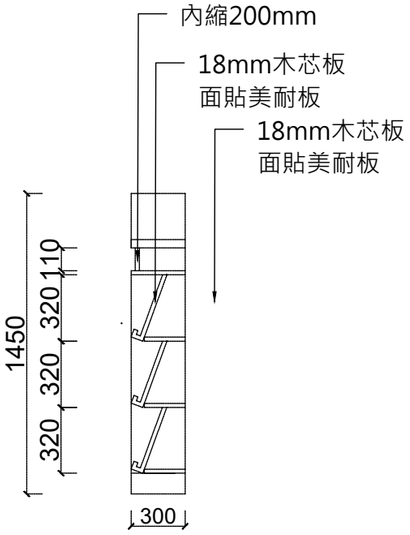


新書/期刊展示櫃

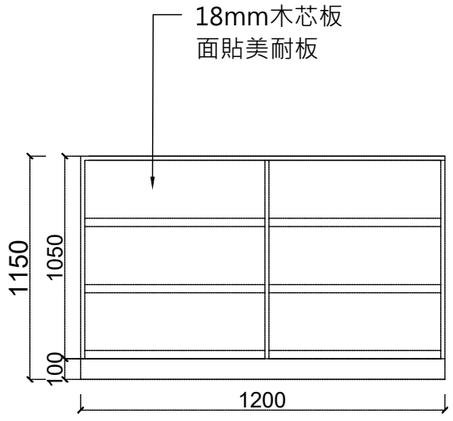


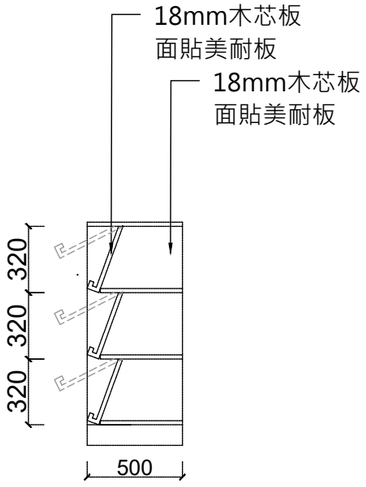

雜誌櫃

造型矮凳

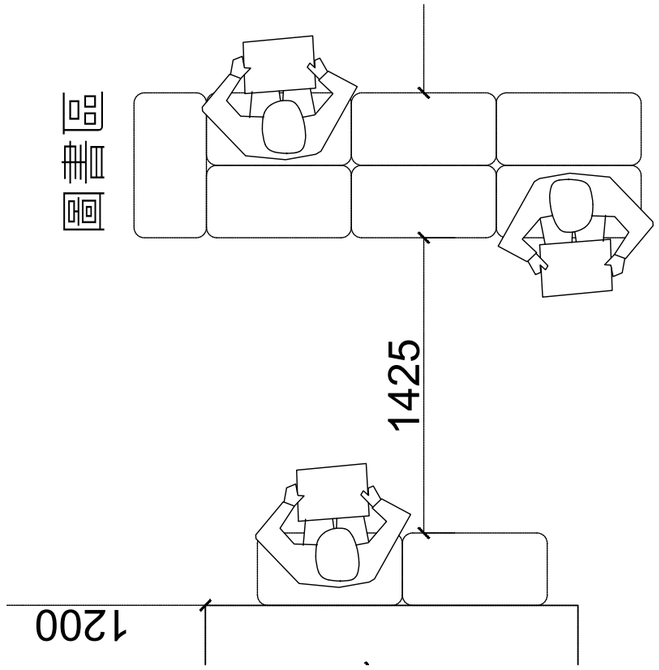

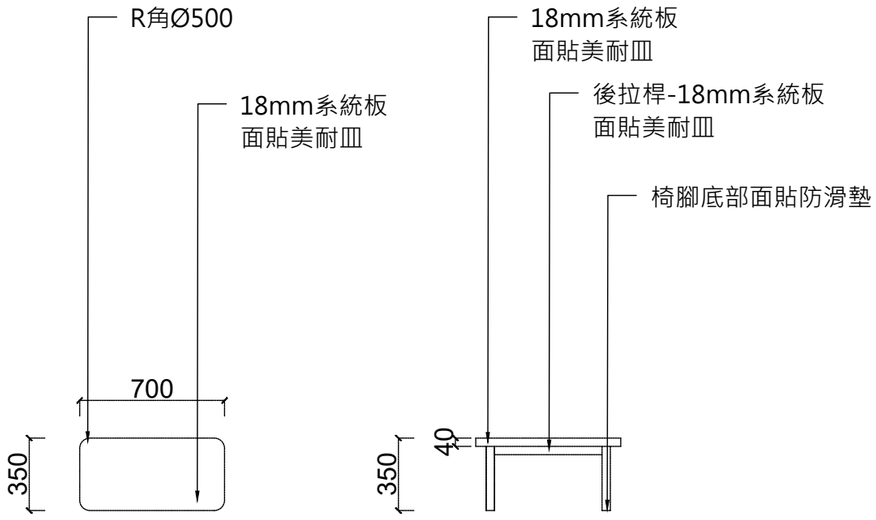

※「單張使用、平面組合、不作垂直堆疊」之方式，以降低兒童攀爬及傾倒風險。
※固定方式:金屬鎖固

※以上圖說設備顏色另選，需與校方或設計單位確認後方可施作。
※依實際狀況調整。

工程名稱 PROJECT

永貞國小圖書館整修工程

圖號 DRAWNG NO.	張號 SHEET NO.
	22/32

圖面修正 REVISISONS

NO.	日期 DATE	內容 REMARKS

圖面名稱 DRAWNGTITLE

造型主題/雜誌書櫃
造型矮凳-設計圖


張薰和建築師事務所
苗栗市國華路158號2樓
電話:037-263019
傳真:037-263851

圖 說 NOTE


起造人及承造人遵守事項
1.起造人於施工前,務請地政機關鑑定界址,
所有尺寸以地政機關鑑界為準,依照實際
基地範圍內配合政府所指定建築線施工,
不得越界侵佔鄰地,更勿僅自先行動工,
而即所有糾紛或受罰,由起造人自行負
法律責任.
2.本設計圖經核准後,起造人及承造人必須
申報開工,按圖施工,並按進度提請查驗
報告,以備完工時申領使用執照.
3.請切實按核准圖樣施工,如原計劃有未盡
理想之處,敬予變更時,務須事先辦理變
更設計手續,經核准後再行施工,以符法
令,切勿擅自變更,而別其後果由起造人
承造人負全責.
4.建造房屋必須請合法且無欠稅之營造廠
承造.
5.所有基礎,樑柱,樓地板,鋼筋,紮妥
後,請起造人知會建築師查驗合格後,才
准灌注混凝土.
6.必須注意鄰居房屋之安全,及行人之安全
,並不可將建築物材料堆置於道路上妨礙
交通.
7.房屋完工後,立即拆除工寮,並將房屋用
圖請路水溝清理修復,然後由承造廠商申
請核發使用執照,再憑使用執照申請接通
水電設備.
8.如有其他臨時發生之疑問,請即提出研討
或向縣市政府建管單位書面查詢,切勿擅
自解釋法令或施做.
9.承造人不得使用下列材料: (1) 海砂
(2) 輻射鋼筋

比例 SCALE	
設計 DESIGN BY	
繪圖 DRAWN BY	
校對 CHECK BY	
核准 APPROVED BY	
日期 DATE	

理書區

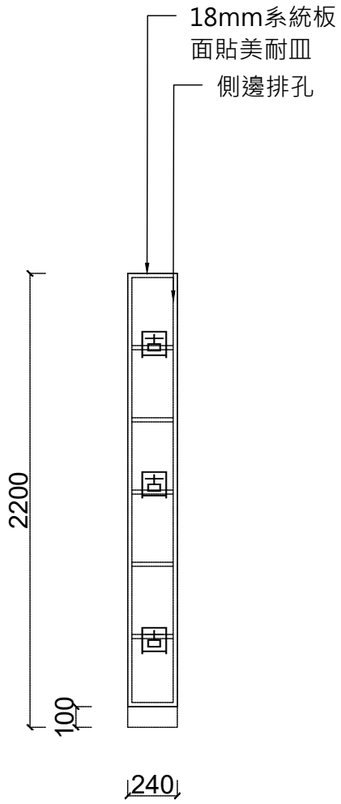


W240*D30*H2200*1座

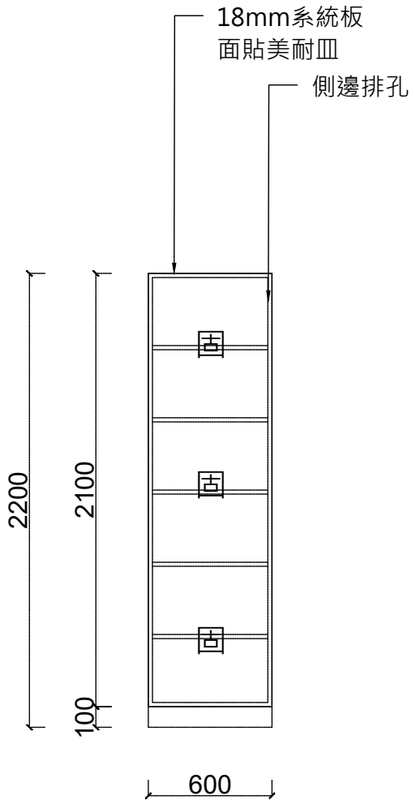


W600*D30*H2200*4座

舞台區

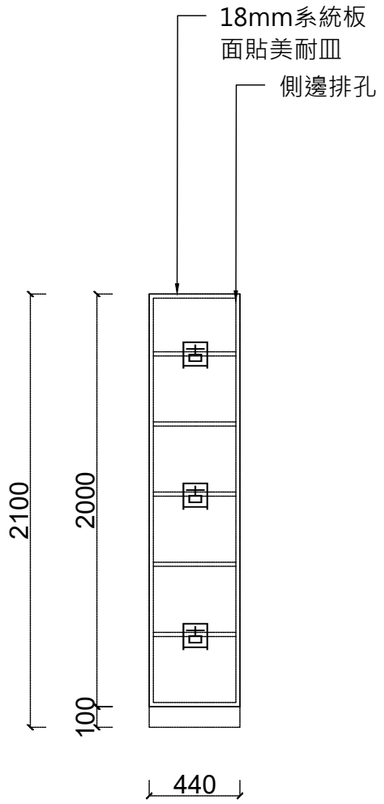

W440*D30*H2100*1座

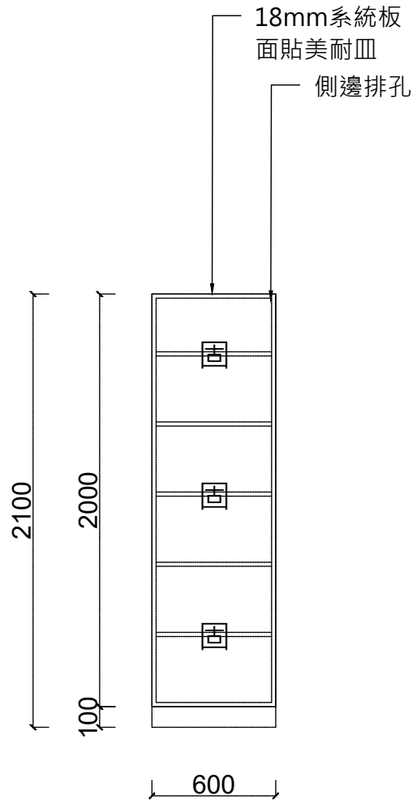

W600*D30*H2100*3座

※以上圖說設備顏色另選，需與校方或設計單位確認後方可施作。
※依實際狀況調整。

工程名稱 PROJECT

永貞國小圖書館整修工程

圖號 DRAWNG NO.	張號 SHEET NO.
	23/32

圖面修正 REVISISONS

NO.	日期 DATE	內容 REMARKS

圖面名稱 DRAWNGTITLE

舞台/理書區高櫃設計圖

張薰和建築師事務所
苗栗市國華路158號2樓
電話:037-263019
傳真:037-263851


圖 說 NOTE

起造人及承造人遵守事項

1.起造人於施工前,務請地政機關鑑定界址,所有尺寸以地政機關鑑界為準,依照實際基地範圍內配合政府所指定建築線施工,不得越界侵佔鄰地,要勿擅自先行動工,否則如有糾紛或受罰,由起造人自行負法律責任.
2.本設計圖經核准後,起造人及承造人必須申報開工,按圖施工,並按進度提請查驗報告,以備完工時申領使用執照.
3.請切實按核准圖樣施工,如原計劃有未盡理想之處,欲予變更時,務須事先辦理變更設計手續,經核准後再行施工,以符法令,切勿擅自變更,否則其後果由起造人承造人負全責.
4.建造房屋必須請合法且無欠稅之營造廠承造.
5.所有基礎,樑柱,樓地板,牆筋,鋼筋,紮妥後,請起造人知會建築師查驗合格後,才准灌注混凝土.
6.必須注意鄰居房屋之安全,及行人之安全,並不可將建築物材料堆置於道路上妨礙交通.
7.房屋完工後,立即拆除工寮,並將房屋周圍道路水溝清理修復,然後由承造廠商申請核發使用執照,再憑使用執照申請接通水電設備.
8.如有其他臨時發生之疑問,請即提出研討或向轄市政府建管單位會商會辦,切勿擅自解釋法令或施做.
9.承造人不得使用下列材料: (1) 海砂
(2) 輻射鋼筋


比例 SCALE	
設計 DESIGN BY	
繪圖 DRAWN BY	
校對 CHECK BY	
核准 APPROVED BY	
日期 DATE	

電信設備櫃(一)

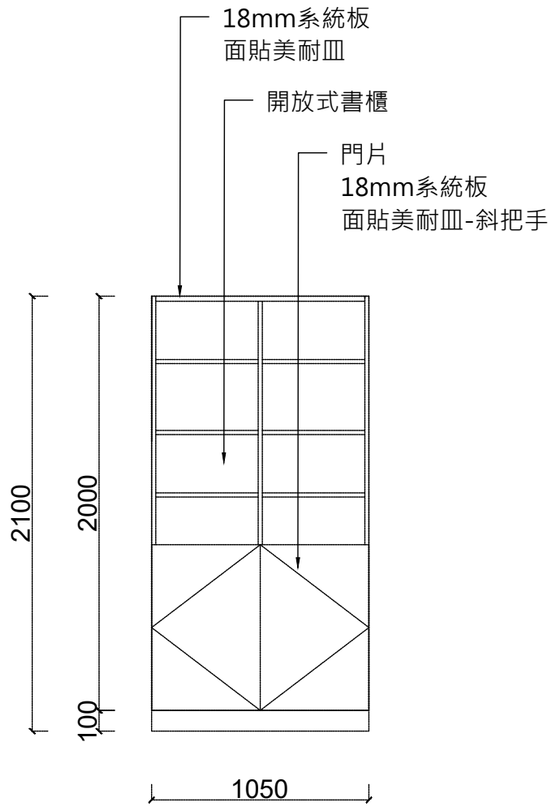

W1050*D30*H2100*1座

電信設備櫃(二)

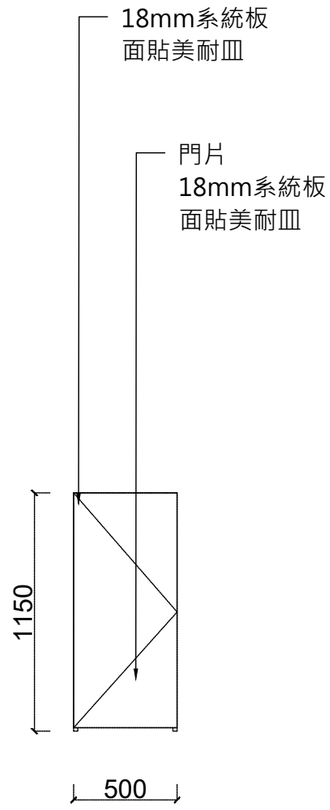

W500*D600*H1150*1座

※以上圖說設備顏色另選，需與校方或設計單位確認後方可施作
※依實際狀況調整。

工程名稱 PROJECT

永貞國小圖書館整修工程

圖號 DRAWNG NO.	張號 SHEET NO.
	24/32

圖面修正 REVISISONS

NO.	日期 DATE	內容 REMARKS

圖面名稱 DRAWNGTITLE

電信設備櫃詳圖

張薰和建築師事務所
苗栗市國華路158號2樓
電話:037-263019
傳真:037-263851

圖 說 NOTE

起造人及承造人遵守事項

1.起造人於施工前,務請地政機關鑑定界址,所有尺寸以地政機關鑑界為準,依照實際基地範圍內配合政府所指定建築線施工,不得越界侵佔鄰地,更勿遷自先行動工,否則所有糾紛或受罰,由起造人自行負法律責任.

2.本設計圖經核准後,起造人及承造人必須申報開工,按圖施工,並按進度提請查驗報告,以備完工時申領使用執照.

3.請切實按核准圖樣施工,如原計劃有未盡理想之處,欲予變更時,務須事先辦理變更設計手續,經核准後再行施工,以符法令,切勿擅自變更,否則其後果由起造人承造人負全責.

4.建造房屋必須請合法且無欠稅之營造廠承造.

5.所有基礎,樑柱,樓地板,鋼筋,紮妥後,請起造人知會建築師查驗合格後,才准灌注混凝土.

6.必須注意鄰居房屋之安全,及行人之安全,並不可將建築物材料堆置於道路上妨礙交通.


7.房屋完工後,立即拆除工寮,並將房屋周圍道路水溝清理修復,然後由承造廠商申請核發使用執照,再憑使用執照申請接通水電設備.

8.如有其他圖詳發生之疑問,請即提出研討或向縣市政府建管單位書面查詢,切勿擅自解釋法令或施做.

9.承造人不得使用下列材料: (1) 海砂 (2) 輻射鋼筋


比例 SCALE	
設計 DESIGN BY	
繪圖 DRAWN BY	
校對 CHECK BY	
核准 APPROVED BY	
日期 DATE	

廣播設備櫃

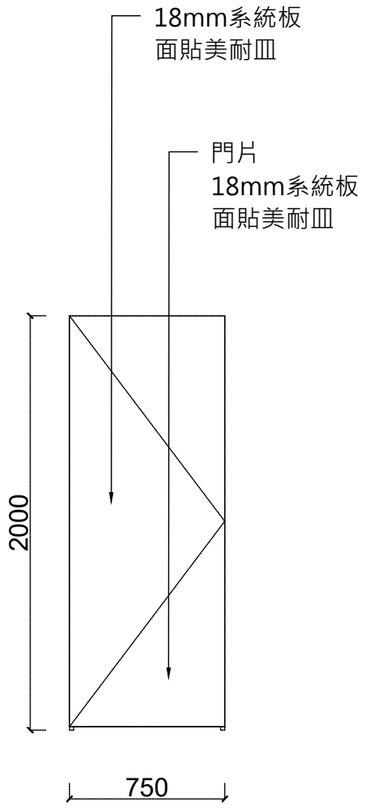

W750*D880*H2000*1座

監視設備櫃

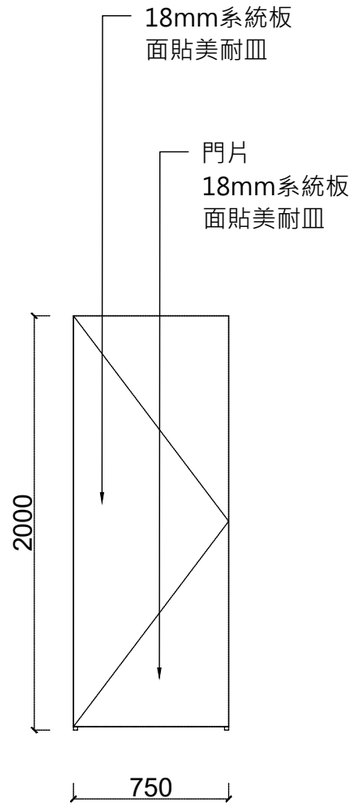

W750*D880*H2000*1座

※以上圖說設備顏色另選，需與校方或設計單位確認後方可施作
※依實際狀況調整。

工程名稱 PROJECT

永貞國小圖書館整修工程

圖號 DRAWNG NO.	張號 SHEET NO.
	25/32

圖面修正 REVISISONS

NO.	日期 DATE	內容 REMARKS

圖面名稱 DRAWNGTITLE

廣播、監視設備櫃設計圖

張薰和建築師事務所

苗栗市國華路158號2樓

電話:037-263019

傳真:037-263851

圖 說 NOTE

起造人及承造人遵守事項

1.起造人於施工前,應請地政機關鑑定界址,所有尺寸以地政機關鑑界為準,依照實際基地範圍內配合政府所指定建築線施工,不得越界侵佔鄰地,要勿擅自先行動工,否則如有糾紛或受罰,由起造人自行負法律責任.

2.本設計圖經核准後,起造人及承造人必須申報開工,按圖施工,並按施度提請查驗報告,以備完工時申領使用執照.

3.請切實按核准圖樣施工,如原計劃有未盡理想之處,欲予變更時,務須事先辦理變更設計手續,經核准後再行施工,以符法令,切勿擅自變更,否則其後果由起造人承造人負全責.

4.建築房屋必須請合法且無欠稅之營造廠承造.

5.所有基礎,樑柱,樓地板,鋼筋,裝妥後,請起造人知會建築師簽驗合格後,才准灌注混凝土.

6.必須注意鄰居房屋之安全,及行人之安全,並不可將建築物材料堆置於道路上妨礙交通.


7.房屋完工後,立即拆除工寮,並將房屋周圍路路水溝清理修復,然後由承造廠商申請核發使用執照,再憑使用執照申請接通水電設備.

8.如有其他圖師發生之疑問,請即提出研討或向縣市政府建管單位書面查詢,切勿擅自解釋法令或施做.

9.承造人不得使用下列材料: (1) 海砂
(2) 輻射鋼筋


比例 SCALE	
設計 DESIGN BY	
繪圖 DRAWN BY	
校對 CHECK BY	
核准 APPROVED BY	
日期 DATE	

保全及電箱設備櫃

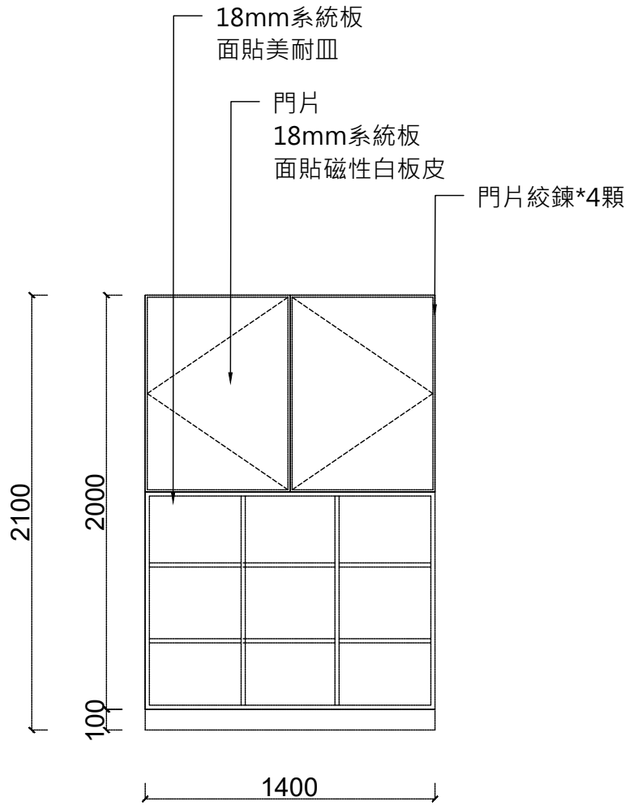


W140*D300*H2100*1座

圖書區

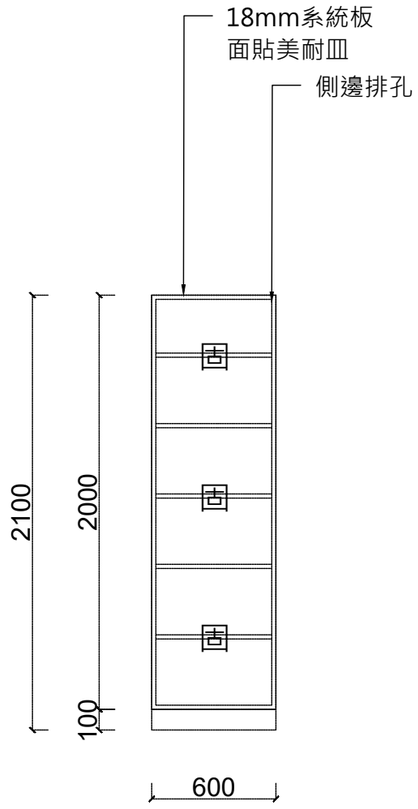

W600*D30*H2100*10座

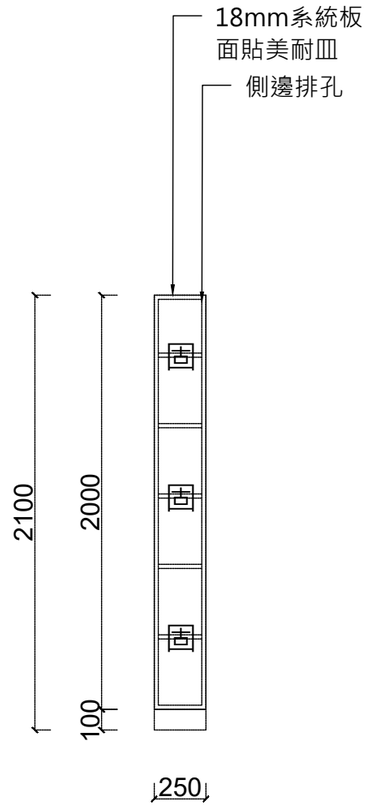

W250*D30*H2100*1座

※以上圖說設備顏色另選，需與校方或設計單位確認後方可施作。
※依實際狀況調整。

工程名稱 PROJECT

永貞國小圖書館整修工程

圖號 DRAWNG NO.	張號 SHEET NO.
	26/32

圖面修正 REVISISONS

NO.	日期 DATE	內容 REMARKS

圖面名稱 DRAWNGTITLE

保全及電箱設備櫃
系統高書櫃設計圖

張薰和建築師事務所
苗栗市國華路158號2樓
電話:037-263019
傳真:037-263851

圖 說 NOTE

起造人及承造人遵守事項

1.起造人於施工前,務請地政機關鑑定界址,所有尺寸以地政機關鑑界為準,依照實際基地範圍內配合政府所指定建築線施工,不得越界侵佔鄰地,更勿擅自先行動工,否則如有糾紛或受罰,由起造人自行負法律責任.

2.本設計圖經核准後,起造人及承造人必須申報開工,按圖施工,並按進度提請查驗報告,以備完工時申領使用執照.

3.請切實按核准圖樣施工,如原計劃有未盡理想之處,欲予變更時,務須事先辦理變更設計手續,經核准後再行施工,以符法令,切勿擅自變更,否則其後果由起造人承造人負全責.

4.建請房屋必須請合法且無欠稅之營造廠承造.

5.所有基礎,樑柱,樓地板,鋼筋,裝妥後,請起造人知會建築師查驗合格後,才准澆注混凝土.

6.必須注意鄰居房屋之安全,及行人之安全,並不可將建築物材料堆置於道路上妨礙交通.


7.房屋完工後,立即拆除工寮,並將房屋周圍路水溝清理修復,然後由承造廠商申請核發使用執照,再憑使用執照申請接通水電設備.

8.如有其他圖詢發生之疑問,請即提出研討或向縣市政府建管單位書面查詢,切勿擅自解釋法令或施做.


9.承造人不得使用下列材料: (1) 海砂
(2) 輻射鋼筋

比例 SCALE	
設計 DESGN BY	
繪圖 DRAWN BY	
校對 CHECK BY	
核准 APPROVED BY	
日期 DATE	

理書區、舞台區、靠窗邊、圖書區-系統開放矮櫃詳圖

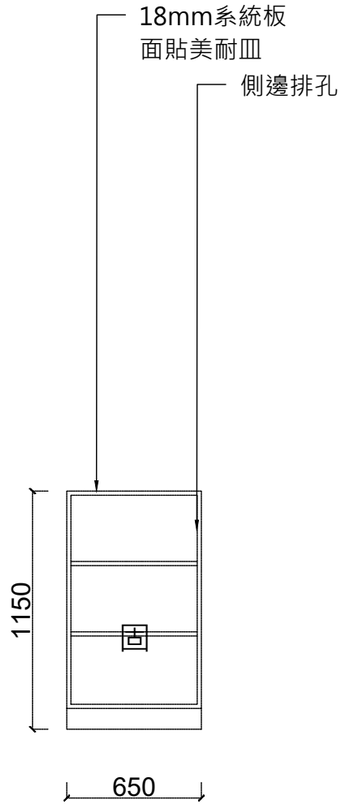

W650*D300*H1150*4座

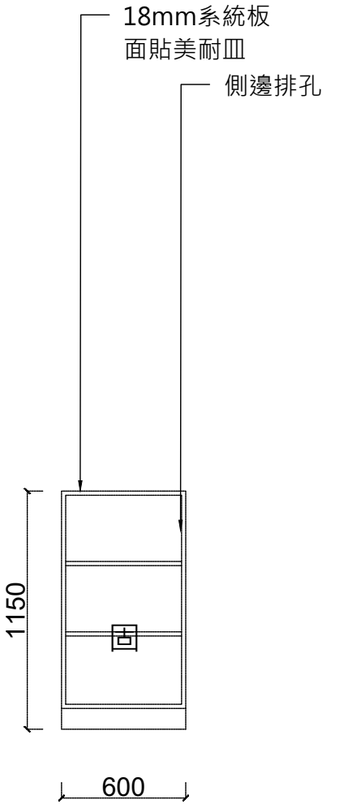

W600*D300*H1150*38座

※以上圖說設備顏色另選，需與校方或設計單位確認後方可施作。
※依實際狀況調整。

工程名稱 PROJECT

永貞國小圖書館整修工程

圖號 DRAWNG NO.

張號 SHEET NO.

27/32

圖面修正 REVISISONS

NO.	日期 DATE	內容 REMARKS

圖面名稱 DRAWNGTITLE

系統矮書櫃設計圖

張薰和建築師事務所

苗栗市國華路158號2樓

電話:037-263019

傳真:037-263851

圖 說 NOTE

起造人及承造人遵守事項

1.起造人於施工前,務請地政機關鑑定界址,所有尺寸以地政機關鑑界為準,依照實際基地範圍內配合政府所指定建築線施工,不得超界侵佔鄰地,更勿遷自先行動工,否則如有糾紛或受罰,由起造人自行負法律責任.

2.本設計圖經核准後,起造人及承造人必須申報開工,按圖施工,並按進度提請查驗報告,以備完工時申領使用執照.

3.請切實按核准圖樣施工,如原計劃有未盡理想之處,欲予變更時,務須事先辦理變更設計手續,經核准後再行施工,以符法令,切勿擅自變更,而別其後果由起造人承造人負全責.

4.建造房屋必須請合法且無欠稅之營造廠承造.

5.所有基礎,樑柱,樓地板,鋼筋,紮妥後,請起造人知會建築師查驗合格後,才准灌注混凝土.

6.必須注意鄰居房屋之安全,及行人之安全,並不可將建築物材料堆置於道路上妨礙交通.

7.房屋完工後,立即拆除工寮,並將房屋用圖路路水溝清理修復,然後由承造廠商申請核發使用執照,再憑使用執照申請接通水電設備.

8.如有其他圖師發生之疑問,請即提出研討或向縣市政府建管單位書面查詢,切勿擅自解釋法令或施做.

9.承造人不得使用下列材料: (1) 海砂 (2) 輻射鋼筋

比例 SCALE	
設計 DESIGN BY	
繪圖 DRAWN BY	
校對 CHECK BY	
核准 APPROVED BY	
日期 DATE	

藤編吊燈





燈具規格說明
尺寸:Ø450mm H220mm 線長600mm
光源:E27x1 16W
材質:藤編
安裝方式:金屬固定件鎖固

燈具規格說明
尺寸:約80公分
光源:E27x1 16W
材質:藤編
安裝方式:金屬固定件鎖固

吸頂圓筒燈




燈具規格說明
尺寸:直徑19cm*高度18cm
燈體材質：壓鑄鋁+壓克力
烤漆顏色:白色/黑色
光源規格：100v-240v全電壓
光源瓦數：E27 20W
色溫：6000K
安裝方式:金屬固定件鎖固

長型吊燈



燈具規格說明
燈具尺寸及材質: L1250mm W150mm H60mm
線長1000mm 鋼板烤漆 擴散板
燈管:T8 LED 20WX2
安裝方式:金屬固定件鎖固

軌道/投射型軌道燈/散光型軌道燈

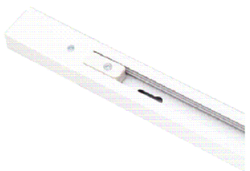

軌道規格說明
材質:鋁合金材質
尺寸:長200CM 寬34CM
高22.2CM
安裝方式:金屬固定件鎖固



燈具規格說明
材質:PC、鐵材質
尺寸:直徑12CM 高22.2CM
色溫:5700K/4000K
光源瓦數：14W*1
光通量:1300LM
演色性:90 ;R9>50
輸入電壓:100V-240V(全電壓)
發光角度:24°
燈體材質:鐵、PC
安裝方式:軌道固定



燈具規格說明
尺寸:寬150mm H260mm
材質:鐵材烤漆(黃)、原木
光源:E27x1 20W
安裝方式:軌道固定

吊扇



吊扇規格說明
馬達規格：AC馬達
電器規格：110V / 60HZ
風段：三段以上
產地：台灣
產品尺寸：52吋
風扇葉數：三片式
備註：吊扇安裝高度須注意，避免運轉中
扇葉陰影遮擋視線
安裝方式:使用專用固定器與金屬固定件鎖固

工程名稱 PROJECT

永貞國小圖書館整修工程

圖號 DRAWNG NO.

張號 SHEET NO.
28/32

圖面修正 REVISISONS

NO.	日期 DATE	內容 REMARKS

圖面名稱 DRAWNGTITLE

燈具及電扇設計圖

張薰和建築師事務所
苗栗市國華路158號2樓
電話:037-263019
傳真:037-263851


圖 說 NOTE

起造人及承造人遵守事項
1.起造人於施工前,務請地政機關鑑定界址,所有尺寸以地政機關鑑界為準,依照實際基地範圍內配合政府所指定建築線施工,不得越界侵佔鄰地,更勿擅自先行動工,否則如有糾紛或受罰,由起造人自行負法律責任。
2.本設計圖經核准後,起造人及承造人必須申報開工,按圖施工,並按進度提請查驗報告,以備完工時申領使用執照。
3.請切實按核准圖樣施工,如原計劃有未盡理想之處,欲予變更時,務須事先辦理變更設計手續,經核准後再行施工,以符法令,切勿擅自變更,否則其後果由起造人承造人負全責。
4.建築房屋必須請合法且無欠稅之營造廠承造。
5.所有基礎,樑柱,樓地板,鋼筋,紮妥後,請起造人知會建築師查驗合格後,才准灌注混凝土。
6.必須注意鄰居房屋之安全,及行人之安全,並不可將建築物材料堆置於道路上妨礙交通。
7.房屋完工後,立即拆除工寮,並將房屋周圍臨路水溝清理修復,然後由承造廠商申請核發使用執照,再憑使用執照申請接通水電設備。
8.如有其他臨時發生之疑問,請即提出研討或向縣市政府建管單位書面查詢,切勿擅自解釋法令或施做。
9.承造人不得使用下列材料: (1) 海砂 (2) 輻射鋼筋


比例 SCALE	
設計 DESIGN BY	
繪圖 DRAWN BY	
校對 CHECK BY	
核准 APPROVED BY	
日期 DATE	

室內牆面、天花板油漆

施工說明:
1.一底二度水泥漆粉刷，一底為批土表面凹縫填平，二度為水泥漆底漆及面漆共二道。
2.油漆均需提送色樣供業主選擇，經監造單位及業主同意後方可施作。
3.提供二年內環保無毒試驗報告。

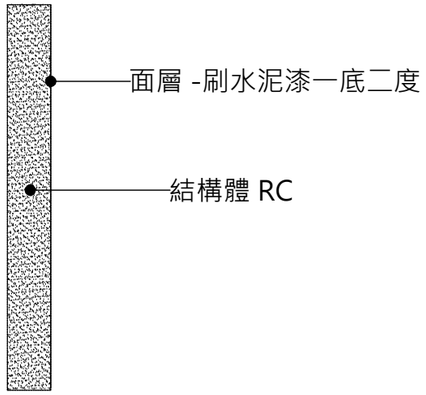



防焰捲簾

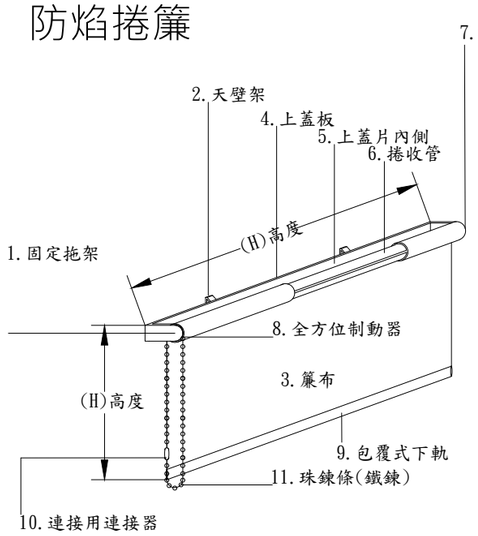


防焰捲簾規範說明:
1.固定拖架:鐵料粉底烤漆
2.天壁架:金屬電鍍
3.簾布:PVC(須通過防焰性測試及合格標示)
4.捲收管:6065-T5直徑35mm鋁合金捲收管
5.旋扭式尾塞:PVC材質旋扭式易於裝卸
6.全方位制動器:採用多方位珠鍊式可旋轉蓋頭, 可做多角度控制其布簾上升下降
採用內至是鋁合金煞車系統,可加強重布止滑(一般採用塑膠易形成磨損造成煞車失靈)
7.包覆式下軌:6065-T5鋁合金材質
8.鏈接用連接器:POM塑膠材質(白色)
9.珠鍊條:圓型
10.需提同近兩年的防焰試驗報告

PVC地磚

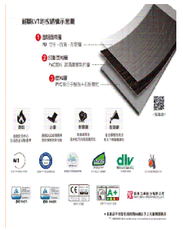

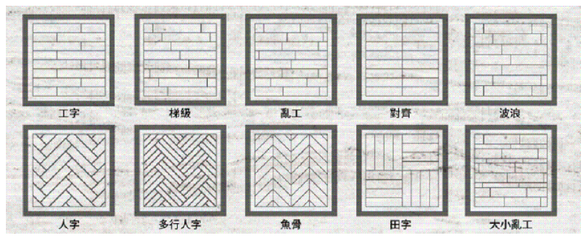

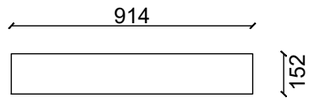

PVC地磚單磚尺寸

規範說明
1.尺寸:寬152.4mm*長914.4mm 厚:2.0mm
2.PVC地磚：性質與尺度應符合契約圖說之規定
3.耐燃性:應符合契約圖說之規定及防焰測報
4.接著劑：除契約圖說另有規定外，鋪貼塑膠地磚用接著劑須符合CNS合格標章
5.安裝方式:依地板專用地板膠黏著
6.備註:尺寸:±0.5cm

窗邊討論桌/檢索桌



規範說明:
尺寸:　1400/1000*400mm
桌板：45mm厚 松木板
桌腳：高溫烤漆打底 表面壓光噴漆
安裝方式:金屬鎖固

工程名稱 PROJECT

永貞國小圖書館整修工程

圖號 DRAWNG NO.	張號 SHEET NO.
	29/32

圖面修正 REVISISONS

NO.	日期 DATE	內容 REMARKS

圖面名稱 DRAWNGTITLE

油漆、防焰捲簾、PVC地磚、窗邊討論桌、檢索桌設計圖


張薰和建築師事務所
苗栗市國華路158號2樓
電話:037-263019
傳真:037-263851

圖 說 NOTE


起造人及承造人遵守事項
1.起造人於施工前,務請地政機關鑑定界址,所有尺寸以地政機關鑑界為準,依照實際基地範圍內配合政府所指定建築線施工,不得越界侵佔鄰地,更勿擅自先行動工,否則如有糾紛或受罰,由起造人自行負法律責任。
2.本設計圖經核准後,起造人及承造人必須申報開工,按圖施工,並按進度提請查驗報告,以備完工時申領使用執照。
3.請切實按核准圖樣施工,如原計劃有未盡理想之處,欲予變更時,務須事先辦理變更設計手續,經核准後再行施工,以符法令,切勿擅自變更,否則其後果由起造人承造人負全責。
4.建造房屋必須請合法且無欠稅之營造廠承造。
5.所有基礎,樑柱,樓地板,鋼筋,紮妥後,請起造人知會建築師簽驗合格後,才准灌注混凝土。
6.必須注意鄰居房屋之安全,及行人之安全,並不可將建築物材料堆置於道路上妨礙交通。
7.房屋完工後,立即拆除工寮,並將房屋周圍路水溝清理修復,然後由承造廠商申請核發使用執照,再憑使用執照申請接通水電設備。
8.如有其他臨時發生之疑問,請即提出研討或向縣市政府建管單位書面查詢,切勿擅自解釋法令或施做。
9.承造人不得使用下列材料: (1) 海砂 (2) 輻射鋼筋


比例 SCALE	
設計 DESIGN BY	
繪圖 DRAWN BY	
校對 CHECK BY	
核准 APPROVED BY	
日期 DATE	


討論區移動式桌子

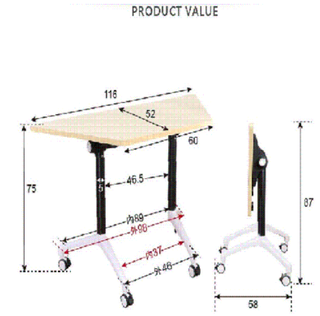



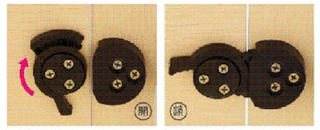

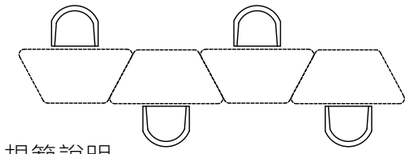

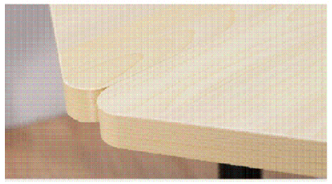

規範說明
尺寸：57 x 75 x 116cm
桌面材質：合成板
支架材質：鐵管烤漆
輪子材質：PU煞車滑輪

櫃檯區辦公椅



規範說明
尺寸：W64×D57×H99~108cm
配件：無枕 / 鋁合金腳 / 附衣架

討論椅



規範說明
名稱：無扶手牛角椅
材質：PP材質

鐵製書報架



規範說明
尺寸：W60 x H109 cm
材質：鐵

工程名稱 PROJECT

永貞國小圖書館整修工程

圖號 DRAWNG NO.	張號 SHEET NO.
	30/32

圖面修正 REVISISONS

NO.	日期 DATE	內容 REMARKS

圖面名稱 DRAWNGTITLE

討論區移動桌、辦公椅、討論椅、書報架詳圖

張薰和建築師事務所
苗栗市國華路158號2樓
電話:037-263019
傳真:037-263851

圖 說 NOTE

起造人及承造人遵守事項

1.起造人於施工前,應請地政機關鑑定界址,所有尺寸以地政機關鑑界為準,依照實際基地範圍內配合政府所指定建築線施工,不得越界侵佔鄰地,要勿擅自先行動工,否則如有糾紛或受罰,由起造人自行負法律責任.
2.本設計圖經核准後,起造人及承造人必須申報開工,按圖施工,並按施度提請查驗報告,以備完工時申領使用執照.
3.請切實按核准圖樣施工,如原計劃有未盡理想之處,致予變更時,務須事先辦理變更設計手續,經核准後再行施工,以符法令,切勿擅自變更,否則其後果由起造人承造人負全責.
4.建築房屋必須請合法且無欠稅之營造廠承造.
5.所有基礎,樑柱,樓地板,鋼筋,裝妥後,請起造人知會建築師簽驗合格後,才准灌注混凝土.
6.必須注意鄰居房屋之安全,及行人之安全,並不可將建築物材料堆置於道路上妨礙交通.
7.房屋完工後,立即拆除工寮,並將房屋周圍道路水溝清理修復,然後由承造廠商申請核發使用執照,再憑使用執照申請接通水電設備.
8.如有其他圖時發生之疑問,請即提出研討或向縣市政府建管單位書面查詢,切勿擅自解釋法令或施做.
9.承造人不得使用下列材料: (1) 海砂 (2) 輻射鋼筋

比例 SCALE	
設計 DESIGN BY	
繪圖 DRAWN BY	
校對 CHECK BY	
核准 APPROVED BY	
日期 DATE	



入口意象-示意圖(一)



入口意象-示意圖(二)



窩居意象-示意圖(一)



窩居意象-示意圖(二)

工程名稱 PROJECT

永貞國小圖書館整修工程

圖號 DRAWNG NO.	張號 SHEET NO.
	31/32

圖面修正 REVISISONS

NO.	日期 DATE	內容 REMARKS

圖面名稱 DRAWNGTITLE

入口意象、造型窩居示意圖

張薰和建築師事務所
苗栗市國華路158號2樓
電話:037-263019
傳真:037-263851

圖 說 NOTE

起造人及承造人遵守事項

1.起造人於施工前,務請地政機關鑑定界址,所有尺寸以地政機關鑑界為準,依照實際基地範圍內配合政府所指定建築線施工,不得越界侵佔鄰地,更勿擅自先行動工,否則因有糾紛或受罰,由起造人自行負法律責任.

2.本設計圖經核准後,起造人及承造人必須申報開工,按圖施工,並按進度提請查驗報告,以備完工時申領使用執照.

3.請切實按核准圖樣施工,如原計劃有未盡理想之處,欲予變更時,務須事先辦理變更設計手續,經核准後再行施工,以符法令,切勿擅自變更,否則其後果由起造人承造人負全責.

4.建造房屋必須請合法且無欠稅之營造廠承造.

5.所有基礎,樑柱,樓地板,鋼筋,紮妥後,請起造人知會建築師查驗合格後,才准灌注混凝土.

6.必須注意鄰居房屋之安全,及行人之安全,並不可將建築物材料堆置於道路上妨礙交通.

7.房屋完工後,立即拆除工寮,並將房屋周圍路水溝清理修復,然後由承造廠商申請核發使用執照,再憑使用執照申請接通水電設備.

8.如有其他圖師發生之疑問,請即提出研討或向縣市政府建管單位書面查詢,切勿擅自解釋法令或臆做.

9.承造人不得使用下列材料: (1) 海砂 (2) 輻射鋼筋

比例 SCALE	
設計 DESIGN BY	
繪圖 DRAWN BY	
校對 CHECK BY	
核准 APPROVED BY	
日期 DATE	



3D示意圖(一)



3D示意圖(二)



3D示意圖(三)



3D示意圖(四)

工程名稱 PROJECT

永貞國小圖書館整修工程

圖號 DRAWNG NO.	張號 SHEET NO.
	32/32

圖面修正 REVISISONS

NO.	日期 DATE	內容 REMARKS

圖面名稱 DRAWNGTITLE

3D示意圖

張薰和建築師事務所

苗栗市國華路158號2樓

電話:037-263019

傳真:037-263851

圖 說 NOTE

起造人及承造人遵守事項

1.起造人於施工前,務請地政機關鑑定界址,所有尺寸以地政機關鑑界為準,依照實際基地範圍內配合政府所指定建築線施工,不得越界侵佔鄰地,更勿擅自先行動工,否則所有糾紛或受罰,由起造人自行負法律責任.

2.本設計圖經核准後,起造人及承造人必須申報開工,按圖施工,並按進度提請查驗報告,以備完工時申領使用執照.

3.請切實按核准圖樣施工,如原計劃有未盡理想之處,欲予變更時,務須事先辦理變更設計手續,經核准後再行施工,以符法令,切勿擅自變更,否則其後果由起造人承造人負責.

4.建造房屋必須請合法且無欠稅之營造廠承造.

5.所有基礎,樑柱,樓地板,鋼筋,紮妥後,請起造人知會建築師查驗合格後,才澆灌注混凝土.

6.必須注意鄰居房屋之安全,及行人之安全,並不可將建築物材料堆置於道路上妨礙交通.

7.房屋完工後,立即拆除工寮,並將房屋周圍道路水溝清理修復,然後由承造廠商申請核發使用執照,再憑使用執照申請接通水電設備.

8.如有其他圖師發生之疑問,請即提出研討或向縣市政府建管單位書面查詢,切勿擅自解釋法令或臆做.

9.承造人不得使用下列材料: (1) 海砂
(2) 輻射鋼筋

比例 SCALE	
設計 DESIGN BY	
繪圖 DRAWN BY	
校對 CHECK BY	
核准 APPROVED BY	
日期 DATE	